

# Bathroom Concept: 9. Fit-out: fixtures and their service points

Bathroom renovation · Bathroom (no site address recorded) · pack 09 of 9 · printed 2026-10-08 · 18 A3 pages

PROPOSED · FOR TRADE REVIEW · NOT AS-BUILT · NOT A COMPLIANCE CERTIFICATE

The bath, reused vanity and toilet, the screen, the wall fittings and the shaving cabinet last, on the tiled room. Wall fittings are set out from the wall's finished face (centreline along it, bottom above the floor), each with its own status. Not recorded yet, so not drawn: the vanity's waste and water (moving about 300 mm right; present positions not measured), the moved GPO, the towel rails' concealed 12 V leads, the bath set's separate hot and cold inlets (not on the set drawing), and the bath waste below the bath. Pipe and cable runs are never drawn.

For: Plumber, Glazier / fit-out.


## How to read these sheets

- Dimensions in millimetres. Every figure carries its status: SC site-confirmed · M measured · PUB published · P proposed · E estimated · DER derived · ENT entered · DEF default · ? unknown. Treat anything not SC or M as a figure to check on site.
- Elevations look at a wall from inside the room; end A is on the left. Wall fittings are set out from the wall's finished (tile) face: centreline along from the return wall's face at A, bottom above the finished floor.
- F1, F2... are the fixtures (fixture schedule in 00-overview.pdf); F11.2 is service point 2 of fixture 11. "?" means not known yet and never drawn.
- Scale 1:20 at A3 on the plans and elevations. Print at 100% ("actual size"), never "fit to page".
- A wall elevation is left out when nothing new is set out on that wall at this stage; the plan and specification still cover the stage. Open decisions and what is still to measure: 00-overview.pdf.

Generated from the project model by npm run printables; the drawings are the same exports saved in the repository (shots/stage-pack, shots/sample-sheets).

## In this pack

| Sheet                          | Page |
|--------------------------------|------|
| Plan                           | 2    |
| Elevation, window wall (north) | 3    |
| Elevation, right wall (east)   | 4    |
| Elevation, left wall (west)    | 5    |
| Specification                  | 6–18 |

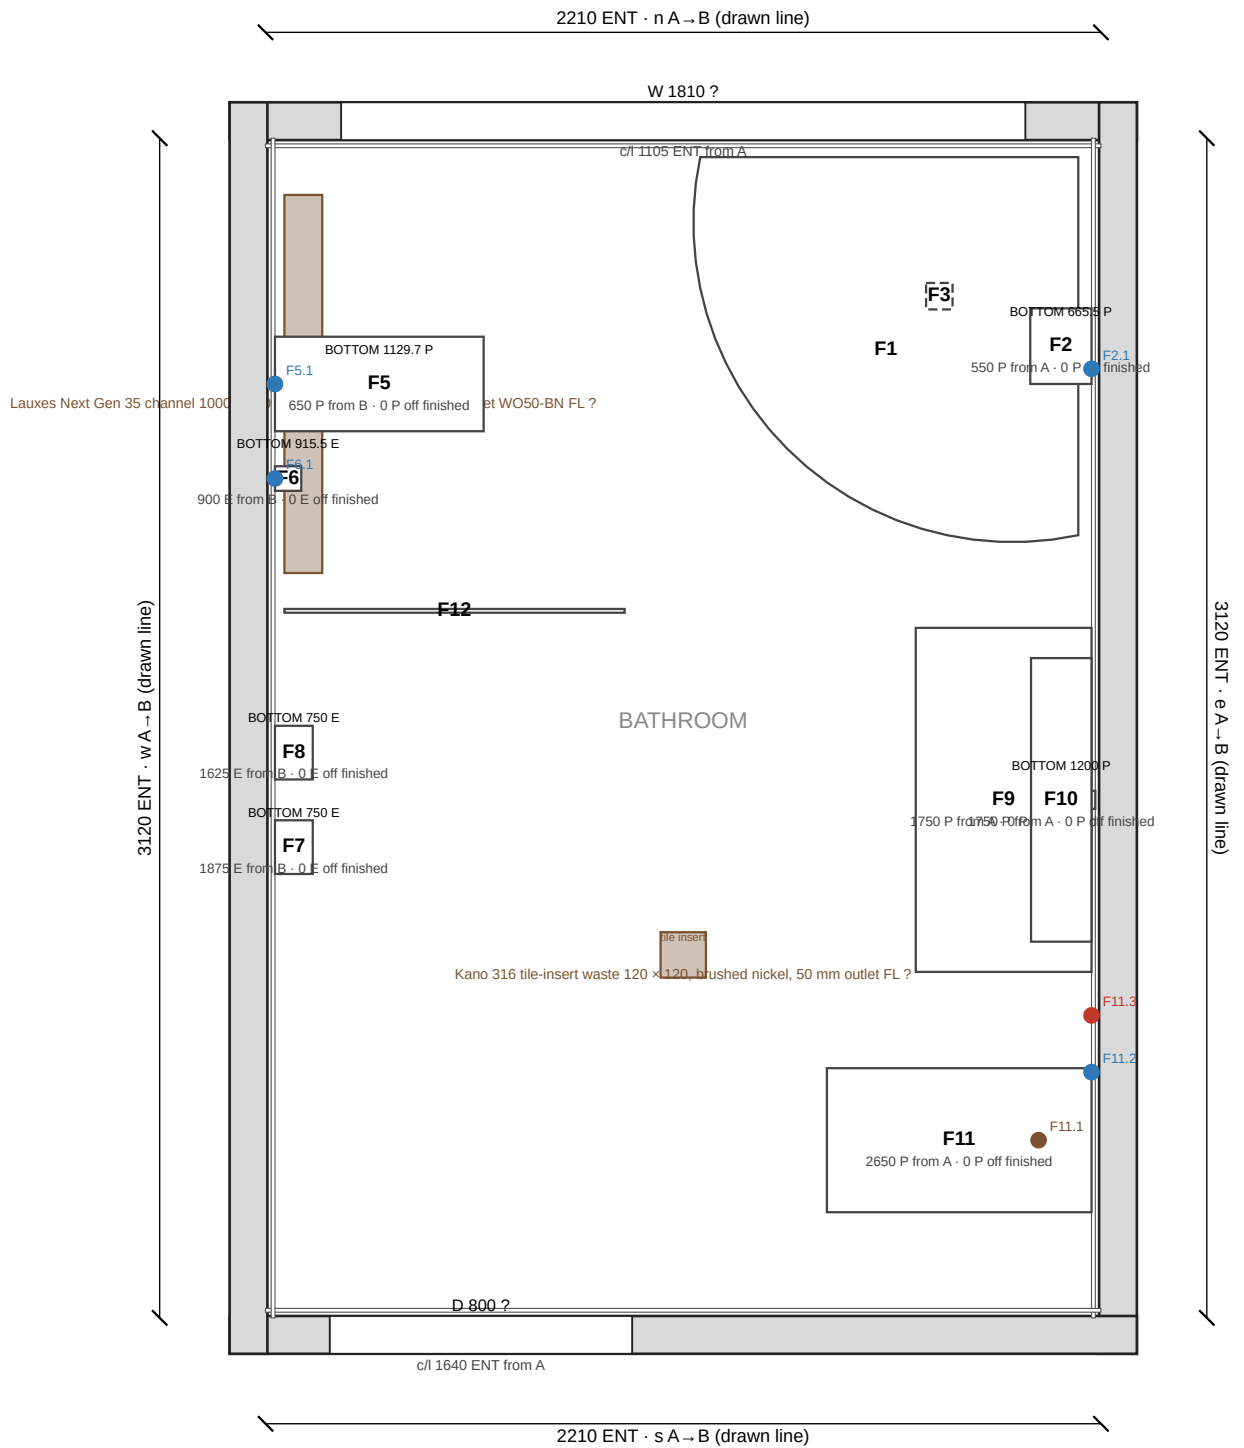

### Stage: 9. Fit-out: fixtures and their service points

Shows 33 element(s) of the one project model; everything else is hidden, not removed.  
Status: SC site-confirmed · M measured · PUB published · P proposed · E estimated · DER derived · ENT entered · DEF default · ? unknown  
Not modelled, never drawn: pipe and cable runs between service points.

#### Fixtures — exact selection

- F1: Enflair Angie Corner 1000mm Bath, GW · Product code SB184-1000GW · Finish unknown · Size / configuration unknown · Handedness unknown · selection purchased  
F2: Enflair Profile III 150mm basin/bath wall mixer set with rectangular plate · Product code K1132-##-150+KDPP32 · Finish unknown · Size / configuration unknown · Handedness unknown · selection purchased  
F3: Ahrok Dome Pop Short Bath Waste 40mm, with pull out basket · Product code SDP-40BN · Finish unknown · Size / configuration unknown · Handedness unknown · selection purchased  
F4: Enflair Profile III petite basin mixer · Product code K1110-31 · Finish unknown · Size / configuration unknown · Handedness unknown · selection purchased  
F5: Profile round twin shower system with adjustable rail · Product code Y1173-31-11-250 · Finish unknown · Size / configuration unknown · Handedness unknown · selection purchased  
F6: Enflair Profile III shower/bath wall mixer · Product code K1130-31 · Finish unknown · Size / configuration unknown · Handedness unknown · selection purchased  
... 6 more: see the specification sheet

#### Wall faces and layers (mm from drawn line)

- Wall n right: 300 × 600 sandy beige matte (Tile Wizards porcelain, colour 'Beige'; code not legible in the photo); thickness 10 E · outer face position 25 E  
Wall e right: 600 × 600 white gloss, a few light grey streaks (Tile Wizards 'Ice' TWJ-14, porcelain); thickness 10 E · outer face position 25 E  
Wall s right: 600 × 600 white gloss, a few light grey streaks (Tile Wizards 'Ice' TWJ-14, porcelain); thickness 10 E · outer face position 25 E  
Wall w right: 600 × 600 white gloss, a few light grey streaks (Tile Wizards 'Ice' TWJ-14, porcelain); thickness 10 E · outer face position 25 E

#### Floor (mm above datum)

- Bathroom floor: substrate: substrate concrete slab, framed in place (house on piers) ENT · substrate top level -120 E · finished level target 0 P · Tiler's screed (heating cable inside) + Tiler's adhesive together, to reach the target 108.5 E  
Bathroom floor: 300 × 600 sandy beige matte (Tile Wizards porcelain, colour 'Beige'; code not legible in the photo); thickness 10 E · top level 0 P

#### Drainage

- Bathroom: Lauxes Next Gen 35 channel 1000 × 100 × 35, brushed nickel, 50 mm outlet WO50-BN: finished level at waste ? · drain product Lauxes Next Gen 35 Custom 1000, brushed nickel NAM · grate length 1000 M · grate width 100 M · outlet diameter 50 M · body depth below grate 35 M · outlet position ?  
Bathroom: Kano 316 tile-insert waste 120 × 120, brushed nickel, 50 mm outlet: finished level at waste ? · drain product Kano 316 Tile Insert Waste 120×120, brushed nickel NAM · grate type tile-insert NAM · grate length 120 M · grate width 120 M · outlet diameter 50 M · body depth below grate ? · outlet position ?

#### Rough-in (as entered, from the named face)

- Bath mixer and spout: Mixer body behind the hub (hot and cold inlets: spacing, size and depth are not on the set drawing): out from finished face 0 P · across from fixture centreline 60 P · up from finished floor 750 P · along from end A 610 P  
Shower system: G1/2 inlet at the upper wall rose (on the rail centreline): out from finished face 0 P · across from fixture centreline 0 P · up from finished floor 1700 P · along from end A 2470 P  
Shower mixer: Mixer body behind the plate (inlet layout and rough-in depth are not on the drawing; about 33.5 mm behind the plate, derived): out from finished face 0 P · across from fixture centreline 0 P · up from finished floor 1000 P · along from end A 2220 E  
Toilet: Pan waste, S-trap (floor): out from finished face 140–260 PUB · across from fixture centreline 0 PUB · up from finished floor ? · along from end A 2650 P  
Toilet: Cold water point (stop tap): out from finished face 0 PUB · across from fixture centreline -180 PUB · up from finished floor 180 PUB · along from end A 2470 P  
Toilet: SpaLet seat power point: out from finished face 0 PUB · across from fixture centreline -330 PUB · up from finished floor 300 PUB · along from end A 2320 P

#### Unresolved in this view (76)

- Bathroom: Lauxes Next Gen 35 channel 1000 × 100 × 35, brushed nickel, 50 mm outlet WO50-BN: finished level at waste (mm) unknown; printed as "?" (missing finished level at waste (mm)).
- Bathroom: Lauxes Next Gen 35 channel 1000 × 100 × 35, brushed nickel, 50 mm outlet WO50-BN: outlet position unknown; printed as "?" (missing outlet position along the channel (entered on the waste), outlet sideways offset (brief)).
- Bathroom: Kano 316 tile-insert waste 120 × 120, brushed nickel, 50 mm outlet: finished level at waste (mm) unknown; printed as "?" (missing finished level at waste (mm)).
- Bathroom: Kano 316 tile-insert waste 120 × 120, brushed nickel, 50 mm outlet: body depth below grate (mm) unknown; printed as "?" (missing installation depth not in the Kano 316 Tile Insert Waste 120×120, brushed nickel brief).
- Bathroom: Kano 316 tile-insert waste 120 × 120, brushed nickel, 50 mm outlet: outlet position unknown; printed as "?" (missing ... more: see the specification sheet / get\_diagram\_view

#### Project: Bathroom Concept

Site / room: Bathroom (no site address recorded)

Stage diagram: 9. Fit-out: fixtures and their service points

Scale 1:20 @ A3 · Exported 2026-10-08 · not a revision of A-01

Prepared by: ? · Plan: Bathroom Concept

PROPOSED · FOR TRADE REVIEW · NOT AS-BUILT · NOT A COMPLIANCE CERTIFICATE

0 1 m  
Scale 1:20 at A3. Orientation not recorded. Dimensions in mm.

Wall n, right side, facing Bathroom. Same visible set as the stage plan; everything else hidden, not removed.

Shown to: finished face (300 × 600 sandy beige matte (Tile Wizards porcelain, colour 'Beige'; code not legible in the photo)), 25 from the drawn line E.

300 × 600 sandy beige matte (Tile Wizards porcelain, colour 'Beige'; code not legible in the photo): 10 E. Extent on the face is not modelled; drawn over the full face.

End A: Finished face of wall\_w (right side) at 25 E along the drawn line.

End B: Finished face of wall\_e (right side) at 2185 E along the drawn line.

Proposed tile set-out: 8 columns × 4 courses, 22 cut pieces (see the wall tiling sheet for cuts).



substrate top -120 E above existing floor surface (current tile top) (flat build-up level)  
300 x 600 sandy beige matte (Tile Wizards porcelain, colour 'Beige'; code not legible in the photo) top 0 P above existing floor surface (current tile top) (flat build-up level)  
Finished floor along this face follows the recorded falls (green); 41 of 41 samples have no plane level.

F1 Corner bath: position along the face ? (no wall set-out recorded) · 0 P to 630 P above existing floor surface (current tile top)  
· stands on the finished floor; height from the kind's envelope

F3 Bath waste: position along the face ? (no wall set-out recorded) · height ? · elevation above the finished floor is not recorded;  
the kind's catalogue stand-in is not used, so it is not drawn

- Corner bath (bath): set-out unknown; printed as "?" (missing not set out from a wall face).
- Corner bath (bath): wasteFromEnd unknown; printed as "?" (missing Sheet gives 520 mm from the right-angle corner along the bisector, not from the end. Along each wall that is  $520/\sqrt{2} \approx 367.7$  mm; that conversion is derived in the host-frame check, not entered as published wasteFromEnd.).
- Corner bath (bath): wasteEnd unknown; printed as "?" (missing Not entered from the cited source.).
- Corner bath (bath): wasteFromSide unknown; printed as "?" (missing Sheet gives 520 mm from the right-angle corner along the bisector, not from the side. Along each wall that is  $520/\sqrt{2} \approx 367.7$  mm; that conversion is derived in the host-frame check, not entered as published wasteFromSide.).
- Corner bath (bath): wasteConnectionDiameter unknown; printed as "?" (missing The Enflair drawing names a Ø50 waste hole, not a pipe connection or outlet size. No connection diameter is entered.).
- Corner bath (bath): surround unknown; printed as "?" (missing Not entered from the cited source.).
- Corner bath (bath): surroundDetail unknown; printed as "?" (missing Not entered from the cited source.).
- Bath waste (bath\_waste): set-out unknown; printed as "?" (missing not set out from a wall face).

... 5 more: see the specification sheet

 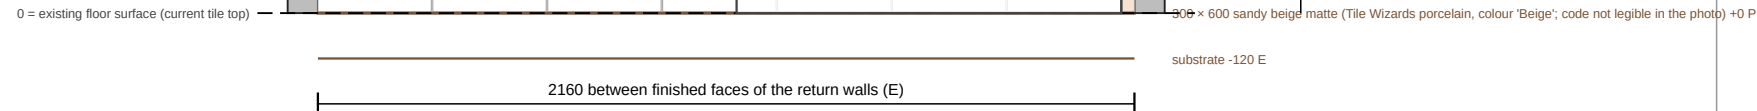


Site / room: Bathroom (no site address recorded)

Stage elevation: 9. Fit-out: fixtures and their service points · wall wall\_n, right side

Scale 1:20 @ A3 · Exported 2026-10-08 · not a revision of A-01

Prepared by: ? · Plan: Bathroom Concept

PROPOSED · FOR TRADE REVIEW · NOT AS-BUILT · NOT A COMPLIANCE CERTIFICATE

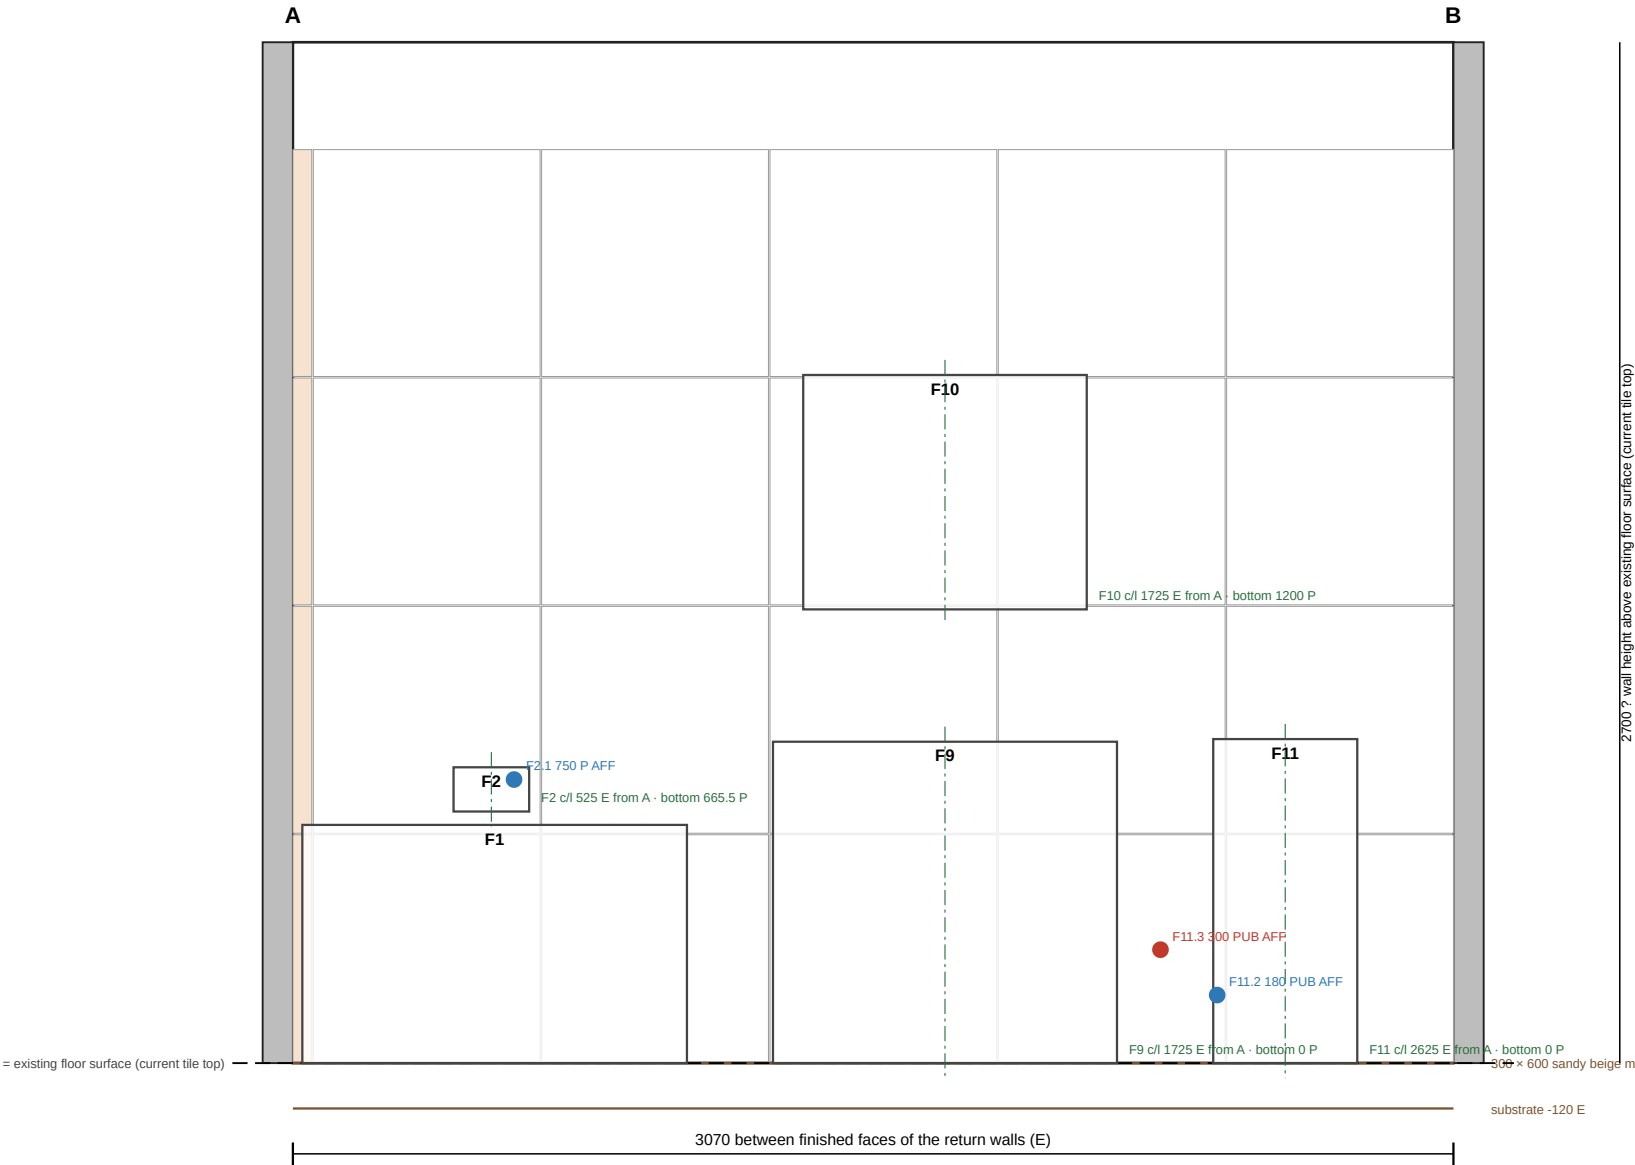

### Stage: 9. Fit-out: fixtures and their service points

Wall e, right side, facing Bathroom. Same visible set as the stage plan; everything else hidden, not removed.  
Status: SC site-confirmed · M measured · PUB published · P proposed · E estimated · DER derived · ENT entered · DEF default · ? unknown

#### This face

Shown to: finished face (600 × 600 white gloss, a few light grey streaks (Tile Wizards 'Ice' TWJ-14, porcelain)), 25 from the drawn line E.  
600 × 600 white gloss, a few light grey streaks (Tile Wizards 'Ice' TWJ-14, porcelain): 10 E. Extent on the face is not modelled; drawn over the full face.  
End A: Finished face of wall\_n (right side) at 25 E along the drawn line.  
End B: Finished face of wall\_s (right side) at 3095 E along the drawn line.  
Proposed tile set-out: 6 columns × 4 courses, 4 cut pieces (see the wall tiling sheet for cuts).

#### Floor at this wall

substrate top -120 E above existing floor surface (current tile top) (flat build-up level)  
300 × 600 sandy beige matte (Tile Wizards porcelain, colour 'Beige'; code not legible in the photo) top 0 P above existing floor surface (current tile top) (flat build-up level)  
Finished floor along this face follows the recorded falls (green); 41 of 41 samples have no plane level.

#### Fixtures against this face

F1 Corner bath: position along the face ? (no wall set-out recorded) · 0 P to 630 P above existing floor surface (current tile top) · stands on the finished floor; height from the kind's envelope  
F2 Bath mixer and spout: 425 E from finished face at A to 625 E · 665.5 P to 782.5 P above existing floor surface (current tile top) · installation height above the named floor datum; bottom is the lever end (envelope bottom); plate centre is the owner's proposed 750 mm; Falls unresolved at this point: height read from the flat finished-floor target.  
F11 Toilet: 2434.5 E from finished face at A to 2815.5 E · 0 P to 857 P above existing floor surface (current tile top) · stands on the finished floor; height from the kind's envelope  
F9 Vanity: 1270 E from finished face at A to 2180 E · 0 P to 850 P above existing floor surface (current tile top) · stands on the finished floor; height from the kind's envelope  
F10 Shaving cabinet: 1350 E from finished face at A to 2100 E · 1200 P to 1820 ? above existing floor surface (current tile top) · installation height above the named floor datum; Falls unresolved at this point: height read from the flat finished-floor target.  
F3 Bath waste: position along the face ? (no wall set-out recorded) · height ? · elevation above the finished floor is not recorded; the kind's catalogue stand-in is not used, so it is not drawn  
F4 Basin mixer: 1701 E from finished face at A to 1749 E · height ? · elevation above the finished floor is not recorded; the kind's catalogue stand-in is not used, so it is not drawn

#### Service points (AFF = above finished floor)

F2.1 water · Mixer body behind the hub (hot and cold inlets: spacing, size and depth are not on the set drawing): 585 E from finished face at A · 750 P above finished floor · 0 P out from finished face  
F11.1 waste · Pan waste, S-trap (floor): 2625 E from finished face at A · up ? · 140–260 PUB out from finished face  
F11.2 water · Cold water point (stop tap): 2445 E from finished face at A · 180 PUB above finished floor · 0 PUB out from finished face  
F11.3 power · SpaLet seat power point: 2295 E from finished face at A · 300 PUB above finished floor · 0 PUB out from finished face


#### Unresolved on this face (36)

- Corner bath (bath): set-out unknown; printed as "?" (missing not set out from a wall face).
- Corner bath (bath): wasteFromEnd unknown; printed as "?" (missing Sheet gives 520 mm from the right-angle corner along the bisector, not from the end. Along each wall that is 520/√2 ≈ 367.7 mm; that conversion is derived in the host-frame check, not entered as published wasteFromEnd.).
- Corner bath (bath): wasteEnd unknown; printed as "?" (missing Not entered from the cited source.).
- Corner bath (bath): wasteFromSide unknown; printed as "?" (missing Sheet gives 520 mm from the right-angle corner along the bisector, not from the side. Along each wall that is 520/√2 ≈ 367.7 mm; that conversion is derived in the host-frame check, not entered as published wasteFromSide.).
- Corner bath (bath): wasteConnectionDiameter unknown; printed as "?" (missing The Enflair drawing names a Ø50 waste hole, not a pipe connection or outlet size. No connection diameter is entered.).
- Corner bath (bath): surround unknown; printed as "?" (missing Not entered from the cited source.).
- Corner bath (bath): surroundDetail unknown; printed as "?" (missing Not entered from the cited source.).
- Bath mixer and spout (bath\_mixer): tapHoles unknown; printed as "?" (missing Not entered from the cited source.).
- ... 28 more: see the specification sheet

#### Project: Bathroom Concept

Site / room: Bathroom (no site address recorded)  
Stage elevation: 9. Fit-out: fixtures and their service points · wall wall\_e, right side  
Scale 1:20 @ A3 · Exported 2026-10-08 · not a revision of A-01  
Prepared by: ? · Plan: Bathroom Concept

PROPOSED · FOR TRADE REVIEW · NOT AS-BUILT · NOT A COMPLIANCE CERTIFICATE

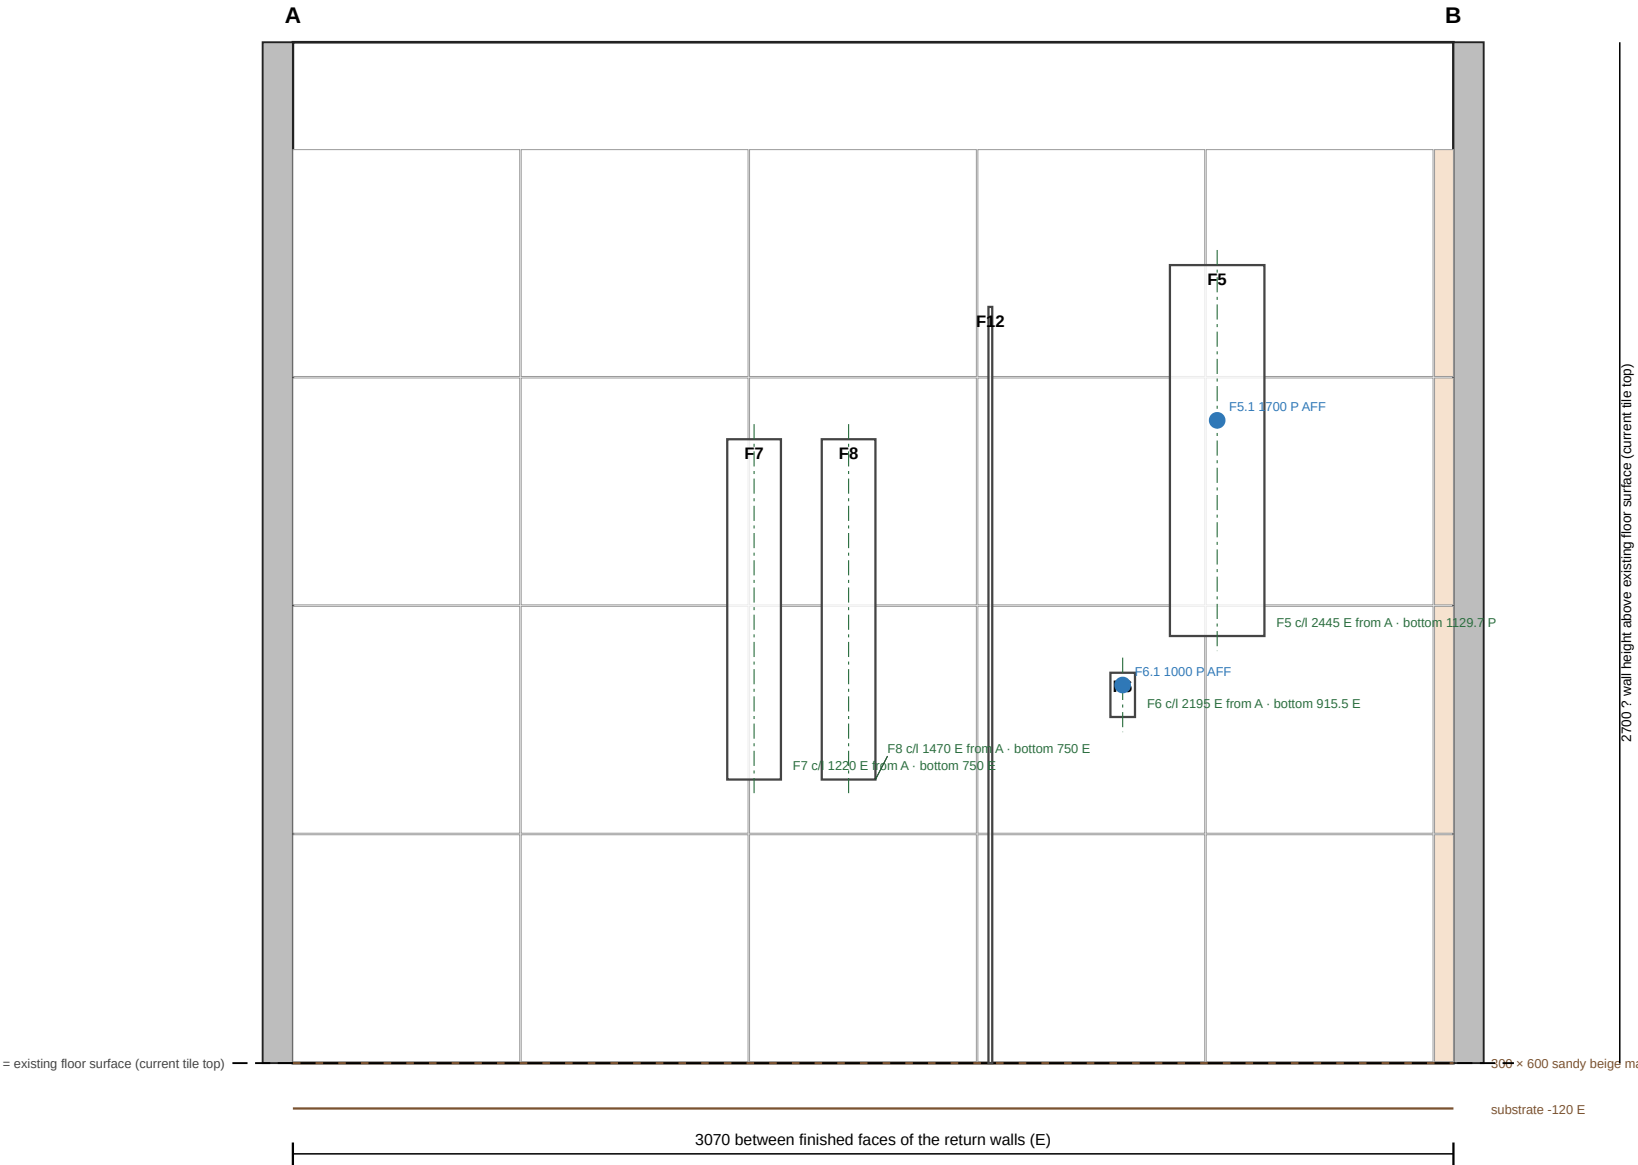

**Stage: 9. Fit-out: fixtures and their service points**

Wall w, right side, facing Bathroom. Same visible set as the stage plan; everything else hidden, not removed.  
Status: SC site-confirmed · M measured · PUB published · P proposed · E estimated · DER derived · ENT entered · DEF default · ? unknown

**This face**

Shown to: finished face (600 × 600 white gloss, a few light grey streaks (Tile Wizards 'Ice' TWJ-14, porcelain)), 25 from the drawn line E.  
600 × 600 white gloss, a few light grey streaks (Tile Wizards 'Ice' TWJ-14, porcelain): 10 E. Extent on the face is not modelled; drawn over the full face.  
End A: Finished face of wall\_s (right side) at 25 E along the drawn line.  
End B: Finished face of wall\_n (right side) at 3095 E along the drawn line.  
Proposed tile set-out: 6 columns × 4 courses, 4 cut pieces (see the wall tiling sheet for cuts).

**Floor at this wall**

substrate top -120 E above existing floor surface (current tile top) (flat build-up level)  
300 × 600 sandy beige matte (Tile Wizards porcelain, colour 'Beige'; code not legible in the photo) top 0 P above existing floor surface (current tile top) (flat build-up level)  
Finished floor along this face follows the recorded falls (green); 41 of 41 samples have no plane level.

**Fixtures against this face**

F12 Fixed glass screen: position along the face ? (no wall set-out recorded) · 0 P to 2000 P above existing floor surface (current tile top) · stands on the finished floor; height from the kind's envelope  
F6 Shower mixer: 2162.5 E from finished face at A to 2227.5 E · 915.5 E to 1032.5 ? above existing floor surface (current tile top) · installation height above the named floor datum; bottom is the lever end (envelope bottom); plate centre is the owner's proposed 1000 mm; Falls unresolved at this point: height read from the flat finished-floor target.  
F5 Shower system: 2320 E from finished face at A to 2570 E · 1129.7 P to 2110.7 P above existing floor surface (current tile top) · installation height above the named floor datum; bottom is the rail foot, 70.3 mm below the lower bracket (derived); lower bracket is the owner's proposed 1200 mm; Falls unresolved at this point: height read from the flat finished-floor target.  
F7 Towel rail: 1149 E from finished face at A to 1291 E · 750 E to 1650 E above existing floor surface (current tile top) · installation height above the named floor datum; Falls unresolved at this point: height read from the flat finished-floor target.  
F8 Towel rail: 1399 E from finished face at A to 1541 E · 750 E to 1650 E above existing floor surface (current tile top) · installation height above the named floor datum; Falls unresolved at this point: height read from the flat finished-floor target.

**Service points (AFF = above finished floor)**

F5.1 water · G1/2 inlet at the upper wall rose (on the rail centreline): 2445 E from finished face at A · 1700 P above finished floor · 0 P out from finished face  
F6.1 water · Mixer body behind the plate (inlet layout and rough-in depth are not on the drawing; about 33.5 mm behind the plate, derived): 2195 E from finished face at A · 1000 P above finished floor · 0 P out from finished face

**Unresolved on this face (35)**

- Shower system (shower\_system): pressureMin unknown; printed as "?" (missing Not entered from the cited source.).
- Shower system (shower\_system): pressureMax unknown; printed as "?" (missing Not entered from the cited source.).
- Shower system (shower\_system): temperatureMax unknown; printed as "?" (missing Not entered from the cited source.).
- Shower system (shower\_system): adjustmentMin unknown; printed as "?" (missing Not entered from the cited source.).
- Shower system (shower\_system): adjustmentMax unknown; printed as "?" (missing Not entered from the cited source.).
- Shower system (shower\_system): inletOffset unknown; printed as "?" (missing Not entered from the cited source.).
- Shower system (shower\_system): inletDepth unknown; printed as "?" (missing Not entered from the cited source.).
- Shower system (shower\_system): inletHeight unknown; printed as "?" (missing Not entered from the cited source.).
- ... 27 more: see the specification sheet

**Project: Bathroom Concept**

Site / room: Bathroom (no site address recorded)  
Stage elevation: 9. Fit-out: fixtures and their service points · wall wall\_w, right side  
Scale 1:20 @ A3 · Exported 2026-10-08 · not a revision of A-01  
Prepared by: ? · Plan: Bathroom Concept

PROPOSED · FOR TRADE REVIEW · NOT AS-BUILT · NOT A COMPLIANCE CERTIFICATE

Specification: 9. Fit-out: fixtures and their service points

Project: Bathroom Concept · Site / room: Bathroom (no site address recorded) · Prepared by: ? · Plan: Bathroom Concept  
Exported 2026-10-08 · not a revision of A-01

PROPOSED · FOR TRADE REVIEW · NOT AS-BUILT · NOT A COMPLIANCE CERTIFICATE

Lists exactly the 33 element(s) visible in this stage view of the one project model. Lengths in mm. Status: SC site-confirmed · M measured · PUB published · P proposed · E estimated · DER derived (converted, not published) · ENT entered (not site-confirmed) · DEF default placeholder · ? unknown. A "?" value is not known and must not be read as a measurement. Not modelled, so never listed: pipe and cable runs between service points (only the points are modelled).

| Element   | Property                           | Value | Status      | Measured from                           | Source                                | Missing |
|---|------------------------------------|-------|-------------|-----------------------------------------|---------------------------------------|---------|
| Walls as drawn (line, length, body)                                                                               |                                    |       |             |                                         |                                       |         |
| Wall n   | length A → B along drawn line (mm) | 2210  | ENT entered |                                         |                                       |         |
|   | thickness (mm)                     | 100   | ? unknown   |                                         |                                       |         |
|   | height (mm)                        | 2700  | ? unknown   |                                         |                                       |         |
| Wall e   | length A → B along drawn line (mm) | 3120  | ENT entered |                                         |                                       |         |
|   | thickness (mm)                     | 100   | ? unknown   |                                         |                                       |         |
|   | height (mm)                        | 2700  | ? unknown   |                                         |                                       |         |
| Wall s   | length A → B along drawn line (mm) | 2210  | ENT entered |                                         |                                       |         |
|   | thickness (mm)                     | 100   | ? unknown   |                                         |                                       |         |
|   | height (mm)                        | 2700  | ? unknown   |                                         |                                       |         |
| Wall w   | length A → B along drawn line (mm) | 3120  | ENT entered |                                         |                                       |         |
|   | thickness (mm)                     | 100   | ? unknown   |                                         |                                       |         |
|   | height (mm)                        | 2700  | ? unknown   |                                         |                                       |         |
| Wall tile   |                                    |       |             |                                         |                                       |         |
| Wall n right: 300 × 600 sandy beige matte (Tile Wizards porcelain, colour 'Beige'; code not legible in the photo) | kind                               | tile  | ENT entered |                                         |                                       |         |
|   | thickness (mm)                     | 10    | E estimated |                                         | owner: 10 mm porcelain, to be checked |         |
|   | outer face position (mm)           | 25    | E estimated | drawn line of wall_n, toward right side |                                       |         |
| Wall e right: 600 × 600 white gloss, a few light grey streaks (Tile Wizards 'Ice' TWJ-14, porcelain)              | kind                               | tile  | ENT entered |                                         |                                       |         |
|   | thickness (mm)                     | 10    | E estimated |                                         | owner: 10 mm porcelain, to be checked |         |
|   | outer face position (mm)           | 25    | E estimated | drawn line of wall_e, toward right side |                                       |         |
| Wall s right: 600 × 600 white gloss, a few light grey streaks (Tile Wizards 'Ice' TWJ-14, porcelain)              | kind                               | tile  | ENT entered |                                         |                                       |         |
|   | thickness (mm)                     | 10    | E estimated |                                         | owner: 10 mm porcelain, to be checked |         |
|   | outer face position (mm)           | 25    | E estimated | drawn line of wall_s, toward right side |                                       |         |
| Wall w right: 600 × 600 white gloss, a few light grey streaks (Tile Wizards 'Ice' TWJ-14, porcelain)              | kind                               | tile  | ENT entered |                                         |                                       |         |
|   | thickness (mm)                     | 10    | E estimated |                                         | owner: 10 mm porcelain, to be checked |         |
|   | outer face position (mm)           | 25    | E estimated | drawn line of wall_w, toward right side |                                       |         |
| Windows   |                                    |       |             |                                         |                                       |         |
| Window window_n on wall_n                                                                                         | width (mm)                         | 1810  | ? unknown   |                                         |                                       |         |
|   | sill above floor (mm)              | 1520  | ? unknown   |                                         |                                       |         |
|   | height (mm)                        | 600   | ? unknown   |                                         |                                       |         |
|   | centre from end A (mm)             | 1105  | ENT entered | wall_n end A, along the drawn line      |                                       |         |
| Doors   |                                    |       |             |                                         |                                       |         |
| Door door_s on wall_s                                                                                             | width (mm)                         | 800   | ? unknown   |                                         |                                       |         |
|   | height (mm)                        | 1900  | ? unknown   |                                         |                                       |         |

| Element   | Property                                                                                    | Value                                                              | Status        | Measured from                                                                       | Source   | Missing                                                                                  |
|---|---------------------------------------------------------------------------------------------|--------------------------------------------------------------------|---------------|-------------------------------------------------------------------------------------|---|------------------------------------------------------------------------------------------|
|   | centre from end A (mm)                                                                      | 1640                                                               | ENT entered   | wall_s end A, along the drawn line                                                  |   |                                                                                          |
| Rooms (outline label)                                                                                               |                                                                                             |                                                                    |               |                                                                                     |   |                                                                                          |
| Room Bathroom   | size w × h (mm)                                                                             | 2110 × 3020                                                        | ENT entered   |                                                                                     |   |                                                                                          |
| Floor substrate and datum                                                                                           |                                                                                             |                                                                    |               |                                                                                     |   |                                                                                          |
| Bathroom floor: substrate                                                                                           | substrate                                                                                   | concrete slab, framed in place (house on piers)                    | ENT entered   |                                                                                     |   |                                                                                          |
|   | substrate top level (mm)                                                                    | -120                                                               | E estimated   | existing floor surface (current tile top)                                           | owner: about 120 mm below the current tile, seen from underneath; confirm after demolition   |                                                                                          |
|   | finished level target (mm)                                                                  | 0                                                                  | P proposed    | existing floor surface (current tile top)                                           | finished tile back at the current tile level, so the doorway stays flush (to confirm)   |                                                                                          |
|   | Tiler's screed (heating cable inside) + Tiler's adhesive together, to reach the target (mm) | 108.5                                                              | E estimated   | substrate top to target                                                             |   |                                                                                          |
| Floor tile   |                                                                                             |                                                                    |               |                                                                                     |   |                                                                                          |
| Bathroom floor: 300 × 600 sandy beige matte (Tile Wizards porcelain, colour 'Beige'; code not legible in the photo) | kind                                                                                        | tile                                                               | ENT entered   |                                                                                     |   |                                                                                          |
|   | thickness (mm)                                                                              | 10                                                                 | E estimated   |                                                                                     | owner: 10 mm porcelain, to be checked   |                                                                                          |
|   | top level (mm)                                                                              | 0                                                                  | P proposed    | existing floor surface (current tile top), read down from the finished-level target |   |                                                                                          |
| Floor wastes   |                                                                                             |                                                                    |               |                                                                                     |   |                                                                                          |
| Bathroom: Lauxes Next Gen 35 channel 1000 × 100 × 35, brushed nickel, 50 mm outlet WO50-BN                          | kind                                                                                        | linear                                                             | ENT entered   |                                                                                     |   |                                                                                          |
|   | finished level at waste (mm)                                                                | ?                                                                  | ? unknown     | existing floor surface (current tile top)                                           |   | finished level at waste (mm)                                                             |
|   | drain product                                                                               | Lauxes Next Gen 35 Custom 1000, brushed nickel                     | NAM named     |                                                                                     |   |                                                                                          |
|   | grate length (mm)                                                                           | 1000                                                               | M measured    |                                                                                     | Photographed packing slip, Surreal Solutions INV-211061 (24 Sep 2026): Next Gen 35 Custom 1000 × 100 × 35 mm; measurement date 2026-10-05; human; metres — 1000 mm custom cut length, end to end                              |                                                                                          |
|   | grate width (mm)                                                                            | 100                                                                | M measured    |                                                                                     | Photographed packing slip, Surreal Solutions INV-211061 (24 Sep 2026): Next Gen 35 Custom 1000 × 100 × 35 mm; measurement date 2026-10-05; human; metres — 100 mm across the channel (BuildMat listing: 100 mm wide)          |                                                                                          |
|   | outlet diameter (mm)                                                                        | 50                                                                 | M measured    |                                                                                     | Photographed packing slip, Surreal Solutions INV-211061 (24 Sep 2026): 1× WO50-BN waste outlet; measurement date 2026-10-05; human; metres — 50 mm outlet; owner found it in the box on 5 Oct 2026                            |                                                                                          |
|   | body depth below grate (mm)                                                                 | 35                                                                 | M measured    | grate top                                                                           | Photographed packing slip, Surreal Solutions INV-211061 (24 Sep 2026): Next Gen 35 Custom 1000 × 100 × 35 mm; measurement date 2026-10-05; human; metres — 35 mm channel depth below the grate (BuildMat listing: 35 mm deep) |                                                                                          |
|   | outlet position                                                                             | ?                                                                  | ? unknown     |                                                                                     |   | outlet position along the channel (entered on the waste), outlet sideways offset (brief) |
| Bathroom: Kano 316 tile-insert waste 120 × 120, brushed nickel, 50 mm outlet                                        | kind                                                                                        | point                                                              | ENT entered   |                                                                                     |   |                                                                                          |
|   | finished level at waste (mm)                                                                | ?                                                                  | ? unknown     | existing floor surface (current tile top)                                           |   | finished level at waste (mm)                                                             |
|   | drain product                                                                               | Kano 316 Tile Insert Waste 120×120, brushed nickel                 | NAM named     |                                                                                     |   |                                                                                          |
|   | grate type                                                                                  | tile-insert                                                        | NAM named     |                                                                                     |   |                                                                                          |
|   | grate length (mm)                                                                           | 120                                                                | M measured    |                                                                                     | Photographed packing slip, Surreal Solutions INV-211061 (24 Sep 2026): KANO 316 Tile Insert Waste 120×120; measurement date 2026-10-05; human; metres                                                                         |                                                                                          |
|   | grate width (mm)                                                                            | 120                                                                | M measured    |                                                                                     | Photographed packing slip, Surreal Solutions INV-211061 (24 Sep 2026): KANO 316 Tile Insert Waste 120×120; measurement date 2026-10-05; human; metres                                                                         |                                                                                          |
|   | outlet diameter (mm)                                                                        | 50                                                                 | M measured    |                                                                                     | Owner's delivery check, 5 Oct 2026: the Kano outlet is 50 mm; measurement date 2026-10-05; human; metres   |                                                                                          |
|   | body depth below grate (mm)                                                                 | ?                                                                  | ? unknown     | grate top                                                                           |   | installation depth not in the Kano 316 Tile Insert Waste 120×120, brushed nickel brief   |
|   | outlet position                                                                             | ?                                                                  | ? unknown     |                                                                                     |   | outlet sideways offset, outlet from body back edge, body depth (envelope) (brief)        |
| Fixtures (bath, vanity, toilet, screen...)                                                                          |                                                                                             |                                                                    |               |                                                                                     |   |                                                                                          |
| Corner bath (bath)                                                                                                  | footprint w × d (mm)                                                                        | 1018 × 1018                                                        | PUB published |                                                                                     |   |                                                                                          |
|   | set-out                                                                                     | ?                                                                  | ? unknown     |                                                                                     |   | not set out from a wall face                                                             |
|   | project selection                                                                           | purchased                                                          | ENT entered   |                                                                                     |   |                                                                                          |
|   | exact product                                                                               | Angie Corner 1000mm Bath, GW (SB184-1000GW) · manufacturer Enflair | ENT entered   |                                                                                     |   |                                                                                          |

| Element                           | Property                                 | Value                                                                            | Status        | Measured from                                                       | Source   | Missing   |
|-----------------------------------|------------------------------------------|----------------------------------------------------------------------------------|---------------|---------------------------------------------------------------------|---|---|
|                                   |                                          | · model Angie Corner 1000mm Bath, GW                                             |               |                                                                     |   |   |
|                                   | Product code                             | SB184-1000GW                                                                     | ENT entered   |                                                                     |   |   |
|                                   | Finish                                   | unknown                                                                          | ? unknown     |                                                                     |   |   |
|                                   | Size / configuration                     | unknown                                                                          | ? unknown     |                                                                     |   |   |
|                                   | Handedness                               | unknown                                                                          | ? unknown     |                                                                     |   |   |
|                                   | components                               | unknown                                                                          | ? unknown     |                                                                     |   |   |
|                                   | length                                   | 1000                                                                             | PUB published | fixture-end                                                         | <a href="https://enflair.com.au/products/angie-1000mm-corner-fit-japanese-soaking-bathtub-gloss-white">https://enflair.com.au/products/angie-1000mm-corner-fit-japanese-soaking-bathtub-gloss-white</a> (SB184-1000 dimension drawing: 1000 mm along each wall side)   |   |
|                                   | width                                    | 1000                                                                             | PUB published | fixture-side                                                        | <a href="https://enflair.com.au/products/angie-1000mm-corner-fit-japanese-soaking-bathtub-gloss-white">https://enflair.com.au/products/angie-1000mm-corner-fit-japanese-soaking-bathtub-gloss-white</a> (SB184-1000 dimension drawing: 1000 mm along each wall side)   |   |
|                                   | height                                   | 630                                                                              | PUB published | finished-floor                                                      | <a href="https://enflair.com.au/products/angie-1000mm-corner-fit-japanese-soaking-bathtub-gloss-white">https://enflair.com.au/products/angie-1000mm-corner-fit-japanese-soaking-bathtub-gloss-white</a> (A-A: 630 mm overall height)   |   |
|                                   | installation                             | corner                                                                           | PUB published |                                                                     | <a href="https://enflair.com.au/products/angie-1000mm-corner-fit-japanese-soaking-bathtub-gloss-white">https://enflair.com.au/products/angie-1000mm-corner-fit-japanese-soaking-bathtub-gloss-white</a> (SB184-1000 dimension drawing: right-angle corner fit)   |   |
|                                   | shape                                    | corner-round                                                                     | PUB published |                                                                     | <a href="https://enflair.com.au/products/angie-1000mm-corner-fit-japanese-soaking-bathtub-gloss-white">https://enflair.com.au/products/angie-1000mm-corner-fit-japanese-soaking-bathtub-gloss-white</a> (SB184-1000: two straight wall sides and a rounded front)   |   |
|                                   | frontWidth                               | 1414.2                                                                           | PUB published | other                                                               | <a href="https://enflair.com.au/products/angie-1000mm-corner-fit-japanese-soaking-bathtub-gloss-white">https://enflair.com.au/products/angie-1000mm-corner-fit-japanese-soaking-bathtub-gloss-white</a> (derived: chord of the two 1000 mm wall sides)   |   |
|                                   | frontProjection                          | 1090                                                                             | PUB published | other                                                               | <a href="https://enflair.com.au/products/angie-1000mm-corner-fit-japanese-soaking-bathtub-gloss-white">https://enflair.com.au/products/angie-1000mm-corner-fit-japanese-soaking-bathtub-gloss-white</a> (section A-A: 1090 mm from the corner to the front of the curve)   |   |
|                                   | wasteFromEnd                             | ?                                                                                | ? unknown     | fixture-end                                                         |   | Sheet gives 520 mm from the right-angle corner along the bisector, not from the end. Along each wall that is $520/\sqrt{2} \approx 367.7$ mm; that conversion is derived in the host-frame check, not entered as published wasteFromEnd.   |
|                                   | wasteEnd                                 | ?                                                                                | ? unknown     |                                                                     |   | Not entered from the cited source.   |
|                                   | wasteFromSide                            | ?                                                                                | ? unknown     | fixture-side                                                        |   | Sheet gives 520 mm from the right-angle corner along the bisector, not from the side. Along each wall that is $520/\sqrt{2} \approx 367.7$ mm; that conversion is derived in the host-frame check, not entered as published wasteFromSide. |
|                                   | wasteFromCorner                          | 520                                                                              | PUB published | other                                                               | <a href="https://enflair.com.au/products/angie-1000mm-corner-fit-japanese-soaking-bathtub-gloss-white">https://enflair.com.au/products/angie-1000mm-corner-fit-japanese-soaking-bathtub-gloss-white</a> (plan: Ø50 waste 520 mm from the corner on the bisector)   |   |
|                                   | wasteHoleDiameter                        | 50                                                                               | PUB published | other                                                               | <a href="https://enflair.com.au/products/angie-1000mm-corner-fit-japanese-soaking-bathtub-gloss-white">https://enflair.com.au/products/angie-1000mm-corner-fit-japanese-soaking-bathtub-gloss-white</a> (plan: Ø50 waste hole)   |   |
|                                   | wasteConnectionDiameter                  | ?                                                                                | ? unknown     | fixture-centreline                                                  |   | The Enflair drawing names a Ø50 waste hole, not a pipe connection or outlet size. No connection diameter is entered.   |
|                                   | overflow                                 | no                                                                               | PUB published |                                                                     | <a href="https://enflair.com.au/products/angie-1000mm-corner-fit-japanese-soaking-bathtub-gloss-white">https://enflair.com.au/products/angie-1000mm-corner-fit-japanese-soaking-bathtub-gloss-white</a> (dimension drawing: no overflow shown)   |   |
|                                   | surround                                 | ?                                                                                | ? unknown     |                                                                     |   | Not entered from the cited source.   |
|                                   | surroundDetail                           | ?                                                                                | ? unknown     |                                                                     |   | Not entered from the cited source.   |
| Bath mixer and spout (bath_mixer) | footprint w × d (mm)                     | 200 × 162                                                                        | PUB published |                                                                     |   |   |
|                                   | set-out                                  | 550 from A · 0 off finished                                                      | P proposed    | wall_e right side, finished face                                    | Owner, 7 Oct 2026: plate centre 500 mm from the window wall, held from the window wall's existing surface as drawn; which face the 500 is measured to is to confirm   |   |
|                                   | installation limitation                  | Falls unresolved at this point: height read from the flat finished-floor target. | ? unknown     |                                                                     |   |   |
|                                   | mounting                                 | wall                                                                             | P proposed    |                                                                     |   |   |
|                                   | product bottom above selected floor (mm) | 665.5                                                                            | P proposed    | Bathroom: finished-floor; existing floor surface (current tile top) | Owner, 7 Oct 2026: plate centre 750 mm above the finished floor tiles (proposed); envelope bottom is the lever end, 84.5 mm below the plate centre (hub radius 22.5 less the 107 mm lever, set drawing)   |   |
|                                   | installed bottom level (mm)              | 665.5                                                                            | P proposed    | Bathroom: finished-floor; existing floor surface (current tile top) | Owner, 7 Oct 2026: plate centre 500 mm from the window wall, held from the window wall's existing surface as drawn; which face the 500 is measured to is to confirm; Owner, 7 Oct 2026: plate centre 750 mm above the finished floor tiles (proposed); envelope bottom is the lever end, 84.5 mm below the plate centre (hub radius 22.5 less the 107 mm lever, set drawing); owner: about 120 mm below the current tile, seen from underneath; confirm after demolition; owner, 7 Oct 2026: liquid polyurethane, about 1.5 mm; owner: 10 mm porcelain, to be checked; owner survey (#1): existing internal surfaces 2110 × 3020 mm; surface-to-frame about 45 mm, seen in one place (#1); owner: guess the framing until demolition; owner's tile and build-up choices; owner: "glue probably 4mm"; the tiler's choice   |   |
|                                   | installed top level (mm)                 | 782.5                                                                            | P proposed    | Bathroom: finished-floor; existing floor surface (current tile top) | Owner, 7 Oct 2026: plate centre 500 mm from the window wall, held from the window wall's existing surface as drawn; which face the 500 is measured to is to confirm; Owner, 7 Oct 2026: plate centre 750 mm above the finished floor tiles (proposed); envelope bottom is the lever end, 84.5 mm below the plate centre (hub radius 22.5 less the 107 mm lever, set drawing); owner: about 120 mm below the current tile, seen from underneath; confirm after demolition; owner, 7 Oct 2026: liquid polyurethane, about 1.5 mm; owner: 10 mm porcelain, to be checked; owner survey (#1): existing internal surfaces 2110 × 3020 mm; surface-to-frame about 45 mm, seen in one place (#1); owner: guess the framing until demolition; owner's tile and build-up choices; owner: "glue probably 4mm"; the tiler's choice; <a href="https://ats.sydney/cdn/shop/files/K1132_-150_KDPP32-ProfileIII150mmBasin_BathWallMixerSetwithRectangularPlate-specification.jpg?v=1757294155&amp;width=2400">https://ats.sydney/cdn/shop/files/K1132_-150_KDPP32-ProfileIII150mmBasin_BathWallMixerSetwithRectangularPlate-specification.jpg?v=1757294155&amp;width=2400</a> (derived: 65 mm plate, hub top 22.5 mm above the plate centre, lever 107 mm from the hub top) |   |

| Element                 | Property             | Value   | Status        | Measured from      | Source   | Missing                            |
|-------------------------|----------------------|---|---------------|--------------------|---|------------------------------------|
|                         | orientation / mirror | 0 degrees / false   | P proposed    |                    |   |                                    |
|                         | geometry basis       | Envelope fallback: no sourced outline supplied; exact planning envelope   | ? unknown     |                    |   |                                    |
|                         | project selection    | purchased   | ENT entered   |                    |   |                                    |
|                         | exact product        | Enflair K1132-31 trim and K1150-31-0-150 spout on one KDPP32 rectangular plate, brushed SS nickel · manufacturer Enflair · model Profile III 150mm basin/bath wall mixer set with rectangular plate | ENT entered   |                    |   |                                    |
|                         | Product code         | K1132-##-150+KDPP32   | ENT entered   |                    |   |                                    |
|                         | Finish               | unknown   | ? unknown     |                    |   |                                    |
|                         | Size / configuration | unknown   | ? unknown     |                    |   |                                    |
|                         | Handedness           | unknown   | ? unknown     |                    |   |                                    |
|                         | components           | documented   | PUB published |                    |   |                                    |
|                         | component 1          | K1132 inner part (in-wall body) · code unknown · quantity unknown · unresolved   | ? unknown     |                    |   |                                    |
|                         | width                | 200   | PUB published | fixture-end        | <a href="https://ats.sydney/cdn/shop/files/K1132-_150_KDPP32-ProfileIII150mmBasin_BathWallMixerSetwithRectangularPlate-specification.jpg?v=1757294155&amp;width=2400">https://ats.sydney/cdn/shop/files/K1132-_150_KDPP32-ProfileIII150mmBasin_BathWallMixerSetwithRectangularPlate-specification.jpg?v=1757294155&amp;width=2400</a> (K1132-##-150+KDPP32 drawing: plate 200 mm)                                                   |                                    |
|                         | depth                | 162   | PUB published | fixture-side       | <a href="https://enflair.com.au/products/profile-iii-150mm-basin-bath-wall-spout-brushed-ss-nickel">https://enflair.com.au/products/profile-iii-150mm-basin-bath-wall-spout-brushed-ss-nickel</a> (derived: 150 mm to the outlet-face centre plus Ø24/2 for the outer lip; the lip itself is not dimensioned)   |                                    |
|                         | height               | 117   | PUB published | fixture-bottom     | <a href="https://ats.sydney/cdn/shop/files/K1132-_150_KDPP32-ProfileIII150mmBasin_BathWallMixerSetwithRectangularPlate-specification.jpg?v=1757294155&amp;width=2400">https://ats.sydney/cdn/shop/files/K1132-_150_KDPP32-ProfileIII150mmBasin_BathWallMixerSetwithRectangularPlate-specification.jpg?v=1757294155&amp;width=2400</a> (derived: 65 mm plate, hub top 22.5 mm above the plate centre, lever 107 mm from the hub top) |                                    |
|                         | mounting             | wall-exposed   | PUB published |                    | <a href="https://ats.sydney/cdn/shop/files/K1132-_150_KDPP32-ProfileIII150mmBasin_BathWallMixerSetwithRectangularPlate-specification.jpg?v=1757294155&amp;width=2400">https://ats.sydney/cdn/shop/files/K1132-_150_KDPP32-ProfileIII150mmBasin_BathWallMixerSetwithRectangularPlate-specification.jpg?v=1757294155&amp;width=2400</a> (K1132-##-150+KDPP32 wall mixer set drawing)                                                  |                                    |
|                         | tapHoles             | ?   | ? unknown     |                    |   | Not entered from the cited source. |
|                         | holeLayout           | ?   | ? unknown     |                    |   | Not entered from the cited source. |
|                         | fixingLayout         | ?   | ? unknown     |                    |   | Not entered from the cited source. |
|                         | pressureMin          | ?   | ? unknown     |                    |   | Not entered from the cited source. |
|                         | pressureMax          | 500 kPa   | M measured    |                    | Photographed K1132-31 label: max static inlet pressure 500 kPa; measurement date 2026-10-05; human; kPa   |                                    |
|                         | temperatureMax       | 80 °C   | M measured    |                    | Photographed K1132-31 label: max hot water 80°; measurement date 2026-10-05; human; °C   |                                    |
|                         | inletMode            | ?   | ? unknown     |                    |   | Not entered from the cited source. |
|                         | inletSpacing         | ?   | ? unknown     | fixture-centreline |   | Not entered from the cited source. |
|                         | waterConnection      | G1/2 in the plate   | PUB published |                    | <a href="https://enflair.com.au/products/profile-iii-150mm-basin-bath-wall-spout-brushed-ss-nickel">https://enflair.com.au/products/profile-iii-150mm-basin-bath-wall-spout-brushed-ss-nickel</a> (K1150-##-0-150 drawing: G1/2 in the cover plate)   |                                    |
|                         | inletOffset          | ?   | ? unknown     | fixture-centreline |   | Not entered from the cited source. |
|                         | inletDepth           | ?   | ? unknown     | fixture-side       |   | Not entered from the cited source. |
|                         | inletHeight          | ?   | ? unknown     | fixture-bottom     |   | Not entered from the cited source. |
|                         | concealedDepthMin    | ?   | ? unknown     | finished-wall      |   | Not entered from the cited source. |
|                         | concealedDepthMax    | ?   | ? unknown     | finished-wall      |   | Not entered from the cited source. |
| Bath waste (bath_waste) | footprint w × d (mm) | 70 × 70   | ENT entered   |                    |   |                                    |
|                         | set-out              | ?   | ? unknown     |                    |   | not set out from a wall face       |
|                         | fitted inside        | bath: 141.3 across its centreline, 367.7 from its back edge   | P proposed    |                    |   |                                    |
|                         | project selection    | purchased   | ENT entered   |                    |   |                                    |
|                         | exact product        | Ahrok SDP-40BN dome pop short bath waste, 40 mm, pull-out basket, brushed nickel · manufacturer Ahrok · model Dome Pop Short Bath Waste 40mm, with pull out basket                                  | ENT entered   |                    |   |                                    |
|                         | Product code         | SDP-40BN   | ENT entered   |                    |   |                                    |
|                         | Finish               | unknown   | ? unknown     |                    |   |                                    |
|                         | Size / configuration | unknown   | ? unknown     |                    |   |                                    |

| Element                   | Property             | Value   | Status           | Measured from      | Source   | Missing                                                                                             |
|---------------------------|----------------------|---|------------------|--------------------|---|---|
|                           | Handedness           | unknown   | ?<br>unknown     |                    |   |   |
|                           | components           | unknown   | ?<br>unknown     |                    |   |   |
|                           | width                | ?   | ?<br>unknown     | fixture-end        |   | Not entered from the cited source.                                                                  |
|                           | depth                | ?   | ?<br>unknown     | fixture-side       |   | Not entered from the cited source.                                                                  |
|                           | height               | ?   | ?<br>unknown     | fixture-bottom     |   | Not entered from the cited source.                                                                  |
|                           | outletDiameter       | ?   | ?<br>unknown     | fixture-centreline |   | Carton prints 40 mm nominal connection; no manufacturer sheet, so not entered as a published figure |
|                           | outletSizeKind       | connection   | PUB<br>published |                    | carton label   |   |
|                           | style                | dome-pop   | M<br>measured    |                    | Photographed carton: Dome Pop Short Bath Waste; measurement date 2026-10-05; human; choice   |   |
|                           | overflow             | ?   | ?<br>unknown     |                    |   | Not entered from the cited source.                                                                  |
|                           | strainer             | pull-out basket   | M<br>measured    |                    | Photographed carton: with pull out basket; measurement date 2026-10-05; human; text   |   |
|                           | certification        | WaterMark licence WM-022812, AS 1589-2001                                                                            | M<br>measured    |                    | Photographed SDP-40BN carton; measurement date 2026-10-05; human; text   |   |
| Basin mixer (basin_mixer) | footprint w × d (mm) | 48 × 145   | PUB<br>published |                    |   |   |
|                           | set-out              | ?   | ?<br>unknown     |                    |   | not set out from a wall face                                                                        |
|                           | fitted inside        | vanity: 0 across its centreline, 62.5 from its back edge                                                             | P<br>proposed    |                    |   |   |
|                           | project selection    | purchased   | ENT<br>entered   |                    |   |   |
|                           | exact product        | Enflair K1110-31 petite basin mixer, brushed SS nickel · manufacturer Enflair · model Profile III petite basin mixer | ENT<br>entered   |                    |   |   |
|                           | Product code         | K1110-31   | ENT<br>entered   |                    |   |   |
|                           | Finish               | unknown   | ?<br>unknown     |                    |   |   |
|                           | Size / configuration | unknown   | ?<br>unknown     |                    |   |   |
|                           | Handedness           | unknown   | ?<br>unknown     |                    |   |   |
|                           | components           | unknown   | ?<br>unknown     |                    |   |   |
|                           | width                | 48   | PUB<br>published | fixture-end        | <a href="https://enflair.com.au/products/profile-iii-petite-basin-mixer-brushed-ss-nickel">https://enflair.com.au/products/profile-iii-petite-basin-mixer-brushed-ss-nickel</a> (K1110 drawing: flange Ø48)                                    |   |
|                           | depth                | 145   | PUB<br>published | fixture-side       | <a href="https://enflair.com.au/products/profile-iii-petite-basin-mixer-brushed-ss-nickel">https://enflair.com.au/products/profile-iii-petite-basin-mixer-brushed-ss-nickel</a> (K1110 drawing: 145 mm back-to-front from the Ø48 flange back) |   |
|                           | height               | 148   | PUB<br>published | fixture-bottom     | <a href="https://enflair.com.au/products/profile-iii-petite-basin-mixer-brushed-ss-nickel">https://enflair.com.au/products/profile-iii-petite-basin-mixer-brushed-ss-nickel</a> (K1110 drawing: 148 mm from the deck/flange to the top)        |   |
|                           | mounting             | deck   | PUB<br>published |                    | <a href="https://enflair.com.au/products/profile-iii-petite-basin-mixer-brushed-ss-nickel">https://enflair.com.au/products/profile-iii-petite-basin-mixer-brushed-ss-nickel</a> (K1110 petite basin mixer, deck-mounted)                       |   |
|                           | tapHoles             | 1   | M<br>measured    |                    | Photographed unit and K1110 drawing: single deck hole, flange Ø48; measurement date 2026-10-05; human; count   |   |
|                           | holeLayout           | Single hole, flange Ø48                                                                                              | PUB<br>published |                    | <a href="https://enflair.com.au/products/profile-iii-petite-basin-mixer-brushed-ss-nickel">https://enflair.com.au/products/profile-iii-petite-basin-mixer-brushed-ss-nickel</a> (K1110 drawing: flange Ø48)                                    |   |
|                           | fixingLayout         | ?   | ?<br>unknown     |                    |   | Not entered from the cited source.                                                                  |
|                           | pressureMin          | ?   | ?<br>unknown     |                    |   | Not entered from the cited source.                                                                  |
|                           | pressureMax          | 500 kPa   | M<br>measured    |                    | Photographed K1110-31 label: max static inlet pressure 500 kPa; measurement date 2026-10-05; human; kPa   |   |
|                           | temperatureMax       | 80 °C   | M<br>measured    |                    | Photographed K1110-31 label: max hot water 80°; measurement date 2026-10-05; human; °C   |   |
|                           | inletMode            | ?   | ?<br>unknown     |                    |   | Not entered from the cited source.                                                                  |
|                           | inletSpacing         | ?   | ?<br>unknown     | fixture-centreline |   | Not entered from the cited source.                                                                  |
|                           | waterConnection      | ?   | ?<br>unknown     |                    |   | Not entered from the cited source.                                                                  |
|                           | inletOffset          | ?   | ?<br>unknown     | fixture-centreline |   | Not entered from the cited source.                                                                  |
|                           | inletDepth           | ?   | ?<br>unknown     | fixture-side       |   | Not entered from the cited source.                                                                  |
|                           | inletHeight          | ?   | ?<br>unknown     | fixture-bottom     |   | Not entered from the cited source.                                                                  |
|                           | concealedDepthMin    | ?   | ?<br>unknown     | finished-wall      |   | Not entered from the cited source.                                                                  |

| Element                       | Property                                 | Value   | Status        | Measured from                                                       | Source   | Missing                            |
|-------------------------------|------------------------------------------|---|---------------|---------------------------------------------------------------------|---|------------------------------------|
|                               | concealedDepthMax                        | ?   | ? unknown     | finished-wall                                                       |   | Not entered from the cited source. |
| Shower system (shower_system) | footprint w × d (mm)                     | 250 × 552   | PUB published |                                                                     |   |                                    |
|                               | set-out                                  | 650 from B · 0 off finished   | P proposed    | wall_w right side, finished face                                    | Centred on the 1200 mm shower (owner: the channel is beneath the shower head, centred on the shower), so 600 mm from the window wall's existing surface as drawn; which face the screen's 1200 is measured to is open   |                                    |
|                               | installation limitation                  | Falls unresolved at this point: height read from the flat finished-floor target.                                                                                        | ? unknown     |                                                                     |   |                                    |
|                               | mounting                                 | wall   | P proposed    |                                                                     |   |                                    |
|                               | product bottom above selected floor (mm) | 1129.7   | P proposed    | Bathroom: finished-floor; existing floor surface (current tile top) | Owner, 7 Oct 2026: lower bracket (rose) centre 1200 mm above the finished floor tiles (proposed, open); envelope bottom is the rail foot, 70.3 mm below it (Y1173 drawing, derived)   |                                    |
|                               | installed bottom level (mm)              | 1129.7   | P proposed    | Bathroom: finished-floor; existing floor surface (current tile top) | Centred on the 1200 mm shower (owner: the channel is beneath the shower head, centred on the shower), so 600 mm from the window wall's existing surface as drawn; which face the screen's 1200 is measured to is open; Owner, 7 Oct 2026: lower bracket (rose) centre 1200 mm above the finished floor tiles (proposed, open); envelope bottom is the rail foot, 70.3 mm below it (Y1173 drawing, derived); owner: about 120 mm below the current tile, seen from underneath; confirm after demolition; owner, 7 Oct 2026: liquid polyurethane, about 1.5 mm; owner: 10 mm porcelain, to be checked; owner survey (#1): existing internal surfaces 2110 × 3020 mm; surface-to-frame about 45 mm, seen in one place (#1); owner: guess the framing until demolition; owner's tile and build-up choices; owner: "glue probably 4mm"; the tiler's choice   |                                    |
|                               | installed top level (mm)                 | 2110.7   | P proposed    | Bathroom: finished-floor; existing floor surface (current tile top) | Centred on the 1200 mm shower (owner: the channel is beneath the shower head, centred on the shower), so 600 mm from the window wall's existing surface as drawn; which face the screen's 1200 is measured to is open; Owner, 7 Oct 2026: lower bracket (rose) centre 1200 mm above the finished floor tiles (proposed, open); envelope bottom is the rail foot, 70.3 mm below it (Y1173 drawing, derived); owner: about 120 mm below the current tile, seen from underneath; confirm after demolition; owner, 7 Oct 2026: liquid polyurethane, about 1.5 mm; owner: 10 mm porcelain, to be checked; owner survey (#1): existing internal surfaces 2110 × 3020 mm; surface-to-frame about 45 mm, seen in one place (#1); owner: guess the framing until demolition; owner's tile and build-up choices; owner: "glue probably 4mm"; the tiler's choice; https://enflair.com.au/products/profile-round-twin-shower-system-with-adjustable-rail-and-250mm-head-brushed-nickel (Y1173 drawing: rail overall 981 mm) |                                    |
|                               | orientation / mirror                     | 0 degrees / false   | P proposed    |                                                                     |   |                                    |
|                               | geometry basis                           | Envelope fallback: no sourced outline supplied; exact planning envelope                                                                                                 | ? unknown     |                                                                     |   |                                    |
|                               | project selection                        | purchased   | ENT entered   |                                                                     |   |                                    |
|                               | exact product                            | Y1173-31-11-250 twin shower, 250 mm rain head, 3F handpiece, brushed nickel · manufacturer unknown · model Profile round twin shower system with adjustable rail        | ENT entered   |                                                                     |   |                                    |
|                               | Product code                             | Y1173-31-11-250   | ENT entered   |                                                                     |   |                                    |
|                               | Finish                                   | unknown   | ? unknown     |                                                                     |   |                                    |
|                               | Size / configuration                     | unknown   | ? unknown     |                                                                     |   |                                    |
|                               | Handedness                               | unknown   | ? unknown     |                                                                     |   |                                    |
|                               | components                               | documented   | PUB published |                                                                     |   |                                    |
|                               | component 1                              | K1130 wall shower/bath mixer, inner part · code unknown · quantity unknown · unresolved                                                                                 | ? unknown     |                                                                     |   |                                    |
|                               | width                                    | 250   | PUB published | fixture-end                                                         | https://enflair.com.au/products/profile-round-twin-shower-system-with-adjustable-rail-and-250mm-head-brushed-nickel (Y1173-##-11-250 drawing: rain head Ø250)   |                                    |
|                               | depth                                    | 552   | PUB published | fixture-side                                                        | https://enflair.com.au/products/profile-round-twin-shower-system-with-adjustable-rail-and-250mm-head-brushed-nickel (derived: 427 mm wall-face to connector centreline plus Ø250/2 to the far edge of the head)   |                                    |
|                               | height                                   | 981   | PUB published | fixture-bottom                                                      | https://enflair.com.au/products/profile-round-twin-shower-system-with-adjustable-rail-and-250mm-head-brushed-nickel (Y1173 drawing: rail overall 981 mm)   |                                    |
|                               | fittingType                              | system   | PUB published |                                                                     | https://enflair.com.au/products/profile-round-twin-shower-system-with-adjustable-rail-and-250mm-head-brushed-nickel (Y1173-##-11-250 twin shower system)   |                                    |
|                               | mounting                                 | wall   | PUB published |                                                                     | https://enflair.com.au/products/profile-round-twin-shower-system-with-adjustable-rail-and-250mm-head-brushed-nickel (Y1173 side view: wall roses Ø55)   |                                    |
|                               | headWidth                                | 250   | PUB published | fixture-centreline                                                  | https://enflair.com.au/products/profile-round-twin-shower-system-with-adjustable-rail-and-250mm-head-brushed-nickel (Y1173-##-11-250 drawing: rain head Ø250)   |                                    |
|                               | armProjection                            | 427   | PUB published | fixture-side                                                        | https://enflair.com.au/products/profile-round-twin-shower-system-with-adjustable-rail-and-250mm-head-brushed-nickel (Y1173 drawing: 427 mm from the mounting/wall face to the rain-head connector centreline)   |                                    |
|                               | railLength                               | 981   | PUB published | fixture-bottom                                                      | https://enflair.com.au/products/profile-round-twin-shower-system-with-adjustable-rail-and-250mm-head-brushed-nickel (Y1173 drawing: rail overall 981 mm)   |                                    |
|                               | fixingLayout                             | Two wall roses Ø55 with 10 mm plates; 500 mm between bracket centres; upper rose 410.7 mm below the rail top; 49 mm from the wall/mounting face to the riser centreline | PUB published |                                                                     | https://enflair.com.au/products/profile-round-twin-shower-system-with-adjustable-rail-and-250mm-head-brushed-nickel (Y1173 drawing: 500 mm bracket centres, 410.7 mm from the top, roses Ø55, plates 10 mm, 49 mm to the riser)   |                                    |
|                               | pressureMin                              | ?   | ? unknown     |                                                                     |   | Not entered from the cited source. |
|                               | pressureMax                              | ?   | ? unknown     |                                                                     |   | Not entered from the cited source. |
|                               | temperatureMax                           | ?   | ? unknown     |                                                                     |   | Not entered from the cited source. |

| Element                     | Property                                 | Value   | Status        | Measured from                                                       | Source   | Missing   |
|-----------------------------|------------------------------------------|---|---------------|---------------------------------------------------------------------|---|---|
|                             | adjustment                               | adjustable   | PUB published |                                                                     | https://enflair.com.au/products/profile-round-twin-shower-system-with-adjustable-rail-and-250mm-head-brushed-nickel (Y1173: adjustable rail / slider)   |   |
|                             | adjustmentMin                            | ?   | ? unknown     | fixture-bottom                                                      |   | Not entered from the cited source.   |
|                             | adjustmentMax                            | ?   | ? unknown     | fixture-bottom                                                      |   | Not entered from the cited source.   |
|                             | waterEntry                               | other   | PUB published |                                                                     | https://enflair.com.au/products/profile-round-twin-shower-system-with-adjustable-rail-and-250mm-head-brushed-nickel (twin outlets: rain head and handpiece)   |   |
|                             | waterConnection                          | G1/2 at the upper wall rose only; rain head and 3F handpiece                                                                             | PUB published |                                                                     | https://enflair.com.au/products/profile-round-twin-shower-system-with-adjustable-rail-and-250mm-head-brushed-nickel (Y1173 drawing: G1/2 at the upper rose, 500 mm above the lower one)   |   |
|                             | inletOffset                              | ?   | ? unknown     | fixture-centreline                                                  |   | Not entered from the cited source.   |
|                             | inletDepth                               | ?   | ? unknown     | fixture-side                                                        |   | Not entered from the cited source.   |
|                             | inletHeight                              | ?   | ? unknown     | fixture-bottom                                                      |   | Not entered from the cited source.   |
| Shower mixer (shower_mixer) | footprint w × d (mm)                     | 65 × 69.5   | ENT entered   |                                                                     |   |   |
|                             | set-out                                  | 900 from B · 0 off finished   | E estimated   | wall_w right side, finished face                                    | Drawn stand-in: where the mixer sits along the shower wall is not chosen (drawn 850 mm from the window wall's existing surface)   |   |
|                             | installation limitation                  | Falls unresolved at this point: height read from the flat finished-floor target.                                                         | ? unknown     |                                                                     |   |   |
|                             | mounting                                 | wall   | P proposed    |                                                                     |   |   |
|                             | product bottom above selected floor (mm) | 915.5   | P proposed    | Bathroom: finished-floor; existing floor surface (current tile top) | Owner, 7 Oct 2026: plate centre 1000 mm above the finished floor tiles (proposed); envelope bottom is the lever end, 84.5 mm below the plate centre (K1130 drawing)   |   |
|                             | installed bottom level (mm)              | 915.5   | E estimated   | Bathroom: finished-floor; existing floor surface (current tile top) | Drawn stand-in: where the mixer sits along the shower wall is not chosen (drawn 850 mm from the window wall's existing surface); Owner, 7 Oct 2026: plate centre 1000 mm above the finished floor tiles (proposed); envelope bottom is the lever end, 84.5 mm below the plate centre (K1130 drawing); owner: about 120 mm below the current tile, seen from underneath; confirm after demolition; owner, 7 Oct 2026: liquid polyurethane, about 1.5 mm; owner: 10 mm porcelain, to be checked; owner survey (#1): existing internal surfaces 2110 × 3020 mm; surface-to-frame about 45 mm, seen in one place (#1); owner: guess the framing until demolition; owner's tile and build-up choices; owner: "glue probably 4mm"; the tiler's choice |   |
|                             | installed top level (mm)                 | 1032.5   | ? unknown     | Bathroom: finished-floor; existing floor surface (current tile top) | Drawn stand-in: where the mixer sits along the shower wall is not chosen (drawn 850 mm from the window wall's existing surface); Owner, 7 Oct 2026: plate centre 1000 mm above the finished floor tiles (proposed); envelope bottom is the lever end, 84.5 mm below the plate centre (K1130 drawing); owner: about 120 mm below the current tile, seen from underneath; confirm after demolition; owner, 7 Oct 2026: liquid polyurethane, about 1.5 mm; owner: 10 mm porcelain, to be checked; owner survey (#1): existing internal surfaces 2110 × 3020 mm; surface-to-frame about 45 mm, seen in one place (#1); owner: guess the framing until demolition; owner's tile and build-up choices; owner: "glue probably 4mm"; the tiler's choice |   |
|                             | orientation / mirror                     | 0 degrees / false   | P proposed    |                                                                     |   |   |
|                             | geometry basis                           | Envelope fallback: no sourced outline supplied; exact planning envelope                                                                  | ? unknown     |                                                                     |   |   |
|                             | project selection                        | purchased   | ENT entered   |                                                                     |   |   |
|                             | exact product                            | Enflair K1130-31 shower mixer trim, round Ø65 plate, brushed SS nickel · manufacturer Enflair · model Profile III shower/bath wall mixer | ENT entered   |                                                                     |   |   |
|                             | Product code                             | K1130-31   | ENT entered   |                                                                     |   |   |
|                             | Finish                                   | unknown   | ? unknown     |                                                                     |   |   |
|                             | Size / configuration                     | unknown   | ? unknown     |                                                                     |   |   |
|                             | Handedness                               | unknown   | ? unknown     |                                                                     |   |   |
|                             | components                               | unknown   | ? unknown     |                                                                     |   |   |
|                             | width                                    | ?   | ? unknown     | fixture-end                                                         |   | Owner's copy of the Enflair K1130 drawing gives plate Ø65; it has no web link, so it is not entered as a published brief figure (the figures are on the measures). |
|                             | depth                                    | ?   | ? unknown     | fixture-side                                                        |   | Owner's copy of the Enflair K1130 drawing gives 65.5 mm lever to plate plus the 4 mm plate; no web link, so not entered as a published brief figure.               |
|                             | height                                   | ?   | ? unknown     | fixture-bottom                                                      |   | Derived from the owner's copy of the Enflair K1130 drawing (Ø65 plate, Ø45 hub, 107 mm lever); no web link, so not entered as a published brief figure.            |
|                             | mounting                                 | ?   | ? unknown     |                                                                     |   | Not entered from the cited source.   |
|                             | tapHoles                                 | ?   | ? unknown     |                                                                     |   | Not entered from the cited source.   |
|                             | holeLayout                               | ?   | ? unknown     |                                                                     |   | Not entered from the cited source.   |

| Element                 | Property                                 | Value   | Status        | Measured from                                                       | Source   | Missing                            |
|-------------------------|------------------------------------------|---|---------------|---------------------------------------------------------------------|---|------------------------------------|
|                         | fixingLayout                             | ?   | ? unknown     |                                                                     |   | Not entered from the cited source. |
|                         | pressureMin                              | ?   | ? unknown     |                                                                     |   | Not entered from the cited source. |
|                         | pressureMax                              | 500 kPa   | M measured    |                                                                     | Photographed K1130 inner-part label: max static inlet pressure 500 kPa; measurement date 2026-10-05; human; kPa   |                                    |
|                         | temperatureMax                           | 80 °C   | M measured    |                                                                     | Photographed K1130 inner-part label: max hot water 80°; measurement date 2026-10-05; human; °C   |                                    |
|                         | inletMode                                | ?   | ? unknown     |                                                                     |   | Not entered from the cited source. |
|                         | inletSpacing                             | ?   | ? unknown     | fixture-centreline                                                  |   | Not entered from the cited source. |
|                         | waterConnection                          | ?   | ? unknown     |                                                                     |   | Not entered from the cited source. |
|                         | inletOffset                              | ?   | ? unknown     | fixture-centreline                                                  |   | Not entered from the cited source. |
|                         | inletDepth                               | ?   | ? unknown     | fixture-side                                                        |   | Not entered from the cited source. |
|                         | inletHeight                              | ?   | ? unknown     | fixture-bottom                                                      |   | Not entered from the cited source. |
|                         | concealedDepthMin                        | ?   | ? unknown     | finished-wall                                                       |   | Not entered from the cited source. |
|                         | concealedDepthMax                        | ?   | ? unknown     | finished-wall                                                       |   | Not entered from the cited source. |
|                         |                                          |   |               |                                                                     |   |                                    |
| Towel rail (towel_rail) | footprint w × d (mm)                     | 142 × 100   | PUB published |                                                                     |   |                                    |
|                         | set-out                                  | 1875 from B · 0 off finished   | E estimated   | wall_w right side, finished face                                    | Drawn stand-in: the rails' places along the left wall are not chosen (drawn 1825 mm from the window wall's existing surface)   |                                    |
|                         | installation limitation                  | Falls unresolved at this point: height read from the flat finished-floor target.   | ? unknown     |                                                                     |   |                                    |
|                         | mounting                                 | wall   | P proposed    |                                                                     |   |                                    |
|                         | product bottom above selected floor (mm) | 750   | P proposed    | Bathroom: finished-floor; existing floor surface (current tile top) | Owner: foot 750 mm above the finished floor tiles (proposed)   |                                    |
|                         | installed bottom level (mm)              | 750   | E estimated   | Bathroom: finished-floor; existing floor surface (current tile top) | Drawn stand-in: the rails' places along the left wall are not chosen (drawn 1825 mm from the window wall's existing surface); Owner: foot 750 mm above the finished floor tiles (proposed); owner: about 120 mm below the current tile, seen from underneath; confirm after demolition; owner, 7 Oct 2026: liquid polyurethane, about 1.5 mm; owner: 10 mm porcelain, to be checked; owner survey (#1): existing internal surfaces 2110 × 3020 mm; surface-to-frame about 45 mm, seen in one place (#1); owner: guess the framing until demolition; owner's tile and build-up choices; owner: "glue probably 4mm"; the tiler's choice   |                                    |
|                         | installed top level (mm)                 | 1650   | E estimated   | Bathroom: finished-floor; existing floor surface (current tile top) | Drawn stand-in: the rails' places along the left wall are not chosen (drawn 1825 mm from the window wall's existing surface); Owner: foot 750 mm above the finished floor tiles (proposed); owner: about 120 mm below the current tile, seen from underneath; confirm after demolition; owner, 7 Oct 2026: liquid polyurethane, about 1.5 mm; owner: 10 mm porcelain, to be checked; owner survey (#1): existing internal surfaces 2110 × 3020 mm; surface-to-frame about 45 mm, seen in one place (#1); owner: guess the framing until demolition; owner's tile and build-up choices; owner: "glue probably 4mm"; the tiler's choice; <a href="https://www.thermogroup.com.au/wp-content/uploads/2021/02/2022-VS900HBN-Specification-Sheet.pdf">https://www.thermogroup.com.au/wp-content/uploads/2021/02/2022-VS900HBN-Specification-Sheet.pdf</a> (VS900HBN specification sheet: H900) |                                    |
|                         | orientation / mirror                     | 0 degrees / false   | P proposed    |                                                                     |   |                                    |
|                         | geometry basis                           | Envelope fallback: no sourced outline supplied; exact planning envelope   | ? unknown     |                                                                     |   |                                    |
|                         | project selection                        | purchased   | ENT entered   |                                                                     |   |                                    |
|                         | exact product                            | Thermorail VS900HBN, 12 V vertical rail, round, brushed nickel, concealed wiring · manufacturer Thermorail · model VS900HBN   | ENT entered   |                                                                     |   |                                    |
|                         | Product code                             | VS900HBN   | ENT entered   |                                                                     |   |                                    |
|                         | Finish                                   | unknown   | ? unknown     |                                                                     |   |                                    |
|                         | Size / configuration                     | unknown   | ? unknown     |                                                                     |   |                                    |
|                         | Handedness                               | unknown   | ? unknown     |                                                                     |   |                                    |
|                         | components                               | unknown   | ? unknown     |                                                                     |   |                                    |
|                         | width                                    | 142   | PUB published | fixture-end                                                         | <a href="https://www.thermogroup.com.au/wp-content/uploads/2021/02/2022-VS900HBN-Specification-Sheet.pdf">https://www.thermogroup.com.au/wp-content/uploads/2021/02/2022-VS900HBN-Specification-Sheet.pdf</a> (VS900HBN specification sheet: Size W142 × H900 × D100)   |                                    |
|                         | depth                                    | 100   | PUB published | fixture-side                                                        | <a href="https://www.thermogroup.com.au/wp-content/uploads/2021/02/2022-VS900HBN-Specification-Sheet.pdf">https://www.thermogroup.com.au/wp-content/uploads/2021/02/2022-VS900HBN-Specification-Sheet.pdf</a> (VS900HBN specification sheet: D100)   |                                    |
|                         | height                                   | 900   | PUB published | fixture-bottom                                                      | <a href="https://www.thermogroup.com.au/wp-content/uploads/2021/02/2022-VS900HBN-Specification-Sheet.pdf">https://www.thermogroup.com.au/wp-content/uploads/2021/02/2022-VS900HBN-Specification-Sheet.pdf</a> (VS900HBN specification sheet: H900)   |                                    |
|                         | fixingLayout                             | 780 mm vertical centres; Ø32 wall roses (thin discs; thickness not on the sheet); Ø25 stems (section; length not on the sheet); removable hook 52 mm from the rail centreline, 19 mm arm section; cap 42 mm wall-to-room (height not on the sheet) | PUB published |                                                                     | <a href="https://www.thermogroup.com.au/wp-content/uploads/2021/02/2022-VS900HBN-Specification-Sheet.pdf">https://www.thermogroup.com.au/wp-content/uploads/2021/02/2022-VS900HBN-Specification-Sheet.pdf</a> (VS900HBN specification sheet: 780 mm centres, Ø32 roses, Ø25 stem section, hook 52 mm from centreline, 19 mm arm section, 42 mm cap depth)   |                                    |
|                         |                                          |   |               |                                                                     |   |                                    |
|                         |                                          |   |               |                                                                     |   |                                    |

| Element                   | Property                                 | Value   | Status        | Measured from                                                       | Source   | Missing                            |
|---------------------------|------------------------------------------|---|---------------|---------------------------------------------------------------------|---|------------------------------------|
|                           | mounting                                 | wall   | PUB published |                                                                     | https://www.thermogroup.com.au/wp-content/uploads/2021/02/2022-VS900HBN-Specification-Sheet.pdf (VS900HBN specification sheet: wall-mounted vertical rail)   |                                    |
|                           | fixingCentresWidth                       | ?   | ? unknown     | fixture-centreline                                                  |   | Not entered from the cited source. |
|                           | fixingCentresHeight                      | 780   | PUB published | fixture-bottom                                                      | https://www.thermogroup.com.au/wp-content/uploads/2021/02/2022-VS900HBN-Specification-Sheet.pdf (VS900HBN specification sheet: 780 mm between fixing centres)   |                                    |
|                           | heating                                  | electric   | PUB published |                                                                     | https://www.thermogroup.com.au/wp-content/uploads/2021/02/2022-VS900HBN-Specification-Sheet.pdf (VS900HBN specification sheet: 12 V, 24 W)   |                                    |
|                           | power                                    | required   | PUB published |                                                                     | https://www.thermogroup.com.au/wp-content/uploads/2021/02/2022-VS900HBN-Specification-Sheet.pdf (VS900HBN specification sheet: 12 V electric)   |                                    |
|                           | powerConnection                          | low-voltage   | PUB published |                                                                     | https://www.thermogroup.com.au/wp-content/uploads/2021/02/2022-VS900HBN-Specification-Sheet.pdf (VS900HBN specification sheet: 12 V)   |                                    |
|                           | powerRequirements                        | 12 V, 24 W; concealed wiring; a transformer is supplied with each rail (owner: both transformers in the ceiling space).   | PUB published |                                                                     | https://www.thermogroup.com.au/wp-content/uploads/2021/02/2022-VS900HBN-Specification-Sheet.pdf (VS900HBN specification sheet: 12 V, 24 W)   |                                    |
|                           | powerOffset                              | ?   | ? unknown     | fixture-centreline                                                  |   | Not entered from the cited source. |
|                           | powerHeight                              | ?   | ? unknown     | fixture-bottom                                                      |   | Not entered from the cited source. |
|                           | powerDepth                               | ?   | ? unknown     | fixture-side                                                        |   | Not entered from the cited source. |
|                           | waterConnection                          | ?   | ? unknown     |                                                                     |   | Not entered from the cited source. |
| Towel rail (towel_rail_2) | footprint w × d (mm)                     | 142 × 100   | PUB published |                                                                     |   |                                    |
|                           | set-out                                  | 1625 from B · 0 off finished   | E estimated   | wall_w right side, finished face                                    | Drawn stand-in: the rails' places along the left wall are not chosen (drawn 1575 mm from the window wall's existing surface)   |                                    |
|                           | installation limitation                  | Falls unresolved at this point: height read from the flat finished-floor target.   | ? unknown     |                                                                     |   |                                    |
|                           | mounting                                 | wall   | P proposed    |                                                                     |   |                                    |
|                           | product bottom above selected floor (mm) | 750   | P proposed    | Bathroom: finished-floor; existing floor surface (current tile top) | Owner: foot 750 mm above the finished floor tiles (proposed)   |                                    |
|                           | installed bottom level (mm)              | 750   | E estimated   | Bathroom: finished-floor; existing floor surface (current tile top) | Drawn stand-in: the rails' places along the left wall are not chosen (drawn 1575 mm from the window wall's existing surface); Owner: foot 750 mm above the finished floor tiles (proposed); owner: about 120 mm below the current tile, seen from underneath; confirm after demolition; owner, 7 Oct 2026: liquid polyurethane, about 1.5 mm; owner: 10 mm porcelain, to be checked; owner survey (#1): existing internal surfaces 2110 × 3020 mm; surface-to-frame about 45 mm, seen in one place (#1); owner: guess the framing until demolition; owner's tile and build-up choices; owner: "glue probably 4mm"; the tiler's choice   |                                    |
|                           | installed top level (mm)                 | 1650   | E estimated   | Bathroom: finished-floor; existing floor surface (current tile top) | Drawn stand-in: the rails' places along the left wall are not chosen (drawn 1575 mm from the window wall's existing surface); Owner: foot 750 mm above the finished floor tiles (proposed); owner: about 120 mm below the current tile, seen from underneath; confirm after demolition; owner, 7 Oct 2026: liquid polyurethane, about 1.5 mm; owner: 10 mm porcelain, to be checked; owner survey (#1): existing internal surfaces 2110 × 3020 mm; surface-to-frame about 45 mm, seen in one place (#1); owner: guess the framing until demolition; owner's tile and build-up choices; owner: "glue probably 4mm"; the tiler's choice; https://www.thermogroup.com.au/wp-content/uploads/2021/02/2022-VS900HBN-Specification-Sheet.pdf (VS900HBN specification sheet: H900) |                                    |
|                           | orientation / mirror                     | 0 degrees / false   | P proposed    |                                                                     |   |                                    |
|                           | geometry basis                           | Envelope fallback: no sourced outline supplied; exact planning envelope   | ? unknown     |                                                                     |   |                                    |
|                           | project selection                        | purchased   | ENT entered   |                                                                     |   |                                    |
|                           | exact product                            | Thermorail VS900HBN, 12 V vertical rail, round, brushed nickel, concealed wiring · manufacturer Thermorail · model VS900HBN   | ENT entered   |                                                                     |   |                                    |
|                           | Product code                             | VS900HBN   | ENT entered   |                                                                     |   |                                    |
|                           | Finish                                   | unknown   | ? unknown     |                                                                     |   |                                    |
|                           | Size / configuration                     | unknown   | ? unknown     |                                                                     |   |                                    |
|                           | Handedness                               | unknown   | ? unknown     |                                                                     |   |                                    |
|                           | components                               | unknown   | ? unknown     |                                                                     |   |                                    |
|                           | width                                    | 142   | PUB published | fixture-end                                                         | https://www.thermogroup.com.au/wp-content/uploads/2021/02/2022-VS900HBN-Specification-Sheet.pdf (VS900HBN specification sheet: Size W142 × H900 × D100)   |                                    |
|                           | depth                                    | 100   | PUB published | fixture-side                                                        | https://www.thermogroup.com.au/wp-content/uploads/2021/02/2022-VS900HBN-Specification-Sheet.pdf (VS900HBN specification sheet: D100)   |                                    |
|                           | height                                   | 900   | PUB published | fixture-bottom                                                      | https://www.thermogroup.com.au/wp-content/uploads/2021/02/2022-VS900HBN-Specification-Sheet.pdf (VS900HBN specification sheet: H900)   |                                    |
|                           | fixingLayout                             | 780 mm vertical centres; Ø32 wall roses (thin discs; thickness not on the sheet); Ø25 stems (section; length not on the sheet); removable hook 52 mm from the rail centreline, 19 mm arm section; cap 42 mm wall-to-room (height not on the sheet) | PUB published |                                                                     | https://www.thermogroup.com.au/wp-content/uploads/2021/02/2022-VS900HBN-Specification-Sheet.pdf (VS900HBN specification sheet: 780 mm centres, Ø32 roses, Ø25 stem section, hook 52 mm from centreline, 19 mm arm section, 42 mm cap depth)   |                                    |

| Element                           | Property                                 | Value   | Status        | Measured from                                                       | Source   | Missing                            |
|-----------------------------------|------------------------------------------|---|---------------|---------------------------------------------------------------------|---|------------------------------------|
|                                   | mounting                                 | wall   | PUB published |                                                                     | https://www.thermogroup.com.au/wp-content/uploads/2021/02/2022-VS900HBN-Specification-Sheet.pdf (VS900HBN specification sheet: wall-mounted vertical rail)   |                                    |
|                                   | fixingCentresWidth                       | ?   | ? unknown     | fixture-centreline                                                  |   | Not entered from the cited source. |
|                                   | fixingCentresHeight                      | 780   | PUB published | fixture-bottom                                                      | https://www.thermogroup.com.au/wp-content/uploads/2021/02/2022-VS900HBN-Specification-Sheet.pdf (VS900HBN specification sheet: 780 mm between fixing centres)   |                                    |
|                                   | heating                                  | electric   | PUB published |                                                                     | https://www.thermogroup.com.au/wp-content/uploads/2021/02/2022-VS900HBN-Specification-Sheet.pdf (VS900HBN specification sheet: 12 V, 24 W)   |                                    |
|                                   | power                                    | required   | PUB published |                                                                     | https://www.thermogroup.com.au/wp-content/uploads/2021/02/2022-VS900HBN-Specification-Sheet.pdf (VS900HBN specification sheet: 12 V electric)   |                                    |
|                                   | powerConnection                          | low-voltage   | PUB published |                                                                     | https://www.thermogroup.com.au/wp-content/uploads/2021/02/2022-VS900HBN-Specification-Sheet.pdf (VS900HBN specification sheet: 12 V)   |                                    |
|                                   | powerRequirements                        | 12 V, 24 W; concealed wiring; a transformer is supplied with each rail (owner: both transformers in the ceiling space). | PUB published |                                                                     | https://www.thermogroup.com.au/wp-content/uploads/2021/02/2022-VS900HBN-Specification-Sheet.pdf (VS900HBN specification sheet: 12 V, 24 W)   |                                    |
|                                   | powerOffset                              | ?   | ? unknown     | fixture-centreline                                                  |   | Not entered from the cited source. |
|                                   | powerHeight                              | ?   | ? unknown     | fixture-bottom                                                      |   | Not entered from the cited source. |
|                                   | powerDepth                               | ?   | ? unknown     | fixture-side                                                        |   | Not entered from the cited source. |
|                                   | waterConnection                          | ?   | ? unknown     |                                                                     |   | Not entered from the cited source. |
| Vanity (vanity)                   | footprint w × d (mm)                     | 910 × 465   | ENT entered   |                                                                     |   |                                    |
|                                   | set-out                                  | 1750 from A · 0 off finished                                                                                            | P proposed    | wall_e right side, finished face                                    | Owner: vanity centred 1700 mm from the window wall (existing surface, as drawn), back to the right wall's finished face; not yet checked against the old position plus 300 mm   |                                    |
|                                   | project selection                        | reused   | ENT entered   |                                                                     |   |                                    |
|                                   | exact product                            | Gloss white floor-standing vanity, ceramic top with integrated basin (reused) · manufacturer unknown · model unknown    | ENT entered   |                                                                     |   |                                    |
|                                   | Product code                             | unknown   | ? unknown     |                                                                     |   |                                    |
|                                   | Finish                                   | unknown   | ? unknown     |                                                                     |   |                                    |
|                                   | Size / configuration                     | unknown   | ? unknown     |                                                                     |   |                                    |
|                                   | Handedness                               | unknown   | ? unknown     |                                                                     |   |                                    |
|                                   | components                               | unknown   | ? unknown     |                                                                     |   |                                    |
| Shaving cabinet (shaving_cabinet) | footprint w × d (mm)                     | 750 × 160   | ENT entered   |                                                                     |   |                                    |
|                                   | set-out                                  | 1750 from A · 0 off finished                                                                                            | P proposed    | wall_e right side, finished face                                    | Owner: centred over the vanity, back to the right wall's finished face   |                                    |
|                                   | installation limitation                  | Falls unresolved at this point: height read from the flat finished-floor target.                                        | ? unknown     |                                                                     |   |                                    |
|                                   | mounting                                 | wall   | P proposed    |                                                                     |   |                                    |
|                                   | product bottom above selected floor (mm) | 1200   | P proposed    | Bathroom: finished-floor; existing floor surface (current tile top) | Owner, 5 Oct 2026: bottom edge 1200 mm, as now, to clear the tap (proposed)   |                                    |
|                                   | installed bottom level (mm)              | 1200   | P proposed    | Bathroom: finished-floor; existing floor surface (current tile top) | Owner: centred over the vanity, back to the right wall's finished face; Owner, 5 Oct 2026: bottom edge 1200 mm, as now, to clear the tap (proposed); owner: about 120 mm below the current tile, seen from underneath; confirm after demolition; owner, 7 Oct 2026: liquid polyurethane, about 1.5 mm; owner: 10 mm porcelain, to be checked; owner survey (#1): existing internal surfaces 2110 × 3020 mm; surface-to-frame about 45 mm, seen in one place (#1); owner: guess the framing until demolition; owner's tile and build-up choices; owner: "glue probably 4mm"; the tiler's choice |                                    |
|                                   | installed top level (mm)                 | 1820   | ? unknown     | Bathroom: finished-floor; existing floor surface (current tile top) | Owner: centred over the vanity, back to the right wall's finished face; Owner, 5 Oct 2026: bottom edge 1200 mm, as now, to clear the tap (proposed); owner: about 120 mm below the current tile, seen from underneath; confirm after demolition; owner, 7 Oct 2026: liquid polyurethane, about 1.5 mm; owner: 10 mm porcelain, to be checked; owner survey (#1): existing internal surfaces 2110 × 3020 mm; surface-to-frame about 45 mm, seen in one place (#1); owner: guess the framing until demolition; owner's tile and build-up choices; owner: "glue probably 4mm"; the tiler's choice |                                    |
|                                   | orientation / mirror                     | 0 degrees / false   | P proposed    |                                                                     |   |                                    |
|                                   | geometry basis                           | Envelope fallback: no sourced outline supplied; exact planning envelope                                                 | ? unknown     |                                                                     |   |                                    |
|                                   | project selection                        | reused   | ENT entered   |                                                                     |   |                                    |
|                                   | exact product                            | Two-door mirror shaving cabinet (reused) · manufacturer unknown · model unknown                                         | ENT entered   |                                                                     |   |                                    |
|                                   | Product code                             | unknown   | ? unknown     |                                                                     |   |                                    |
|                                   | Finish                                   | unknown   | ? unknown     |                                                                     |   |                                    |

| Element   | Property                            | Value   | Status           | Measured from                       | Source   | Missing                      |
|---|-------------------------------------|---|------------------|-------------------------------------|---|------------------------------|
|   | Size / configuration                | unknown   | ?<br>unknown     |                                     |   |                              |
|   | Handedness                          | unknown   | ?<br>unknown     |                                     |   |                              |
|   | components                          | unknown   | ?<br>unknown     |                                     |   |                              |
| Toilet (toilet)   | footprint w × d (mm)                | 381 × 700   | ENT<br>entered   |                                     |   |                              |
|   | set-out                             | 2650 from A · 0 off finished   | P<br>proposed    | wall_e right side,<br>finished face | Owner, 7 Oct 2026: the suite moves to the plan position, 2600 mm from the window wall's existing surface to its centreline; back-to-wall, so its back is on the right wall's finished face |                              |
|   | project selection                   | reused   | ENT<br>entered   |                                     |   |                              |
|   | exact product                       | American Standard Cygnet Over-height Square back-to-wall suite with SpaLet E-bidet seat (reused, moved) · manufacturer American Standard · model Cygnet Hygiene Rim Over-height Square close coupled back-to-wall toilet suite, bottom inlet, with SpaLet E-bidet seat | ENT<br>entered   |                                     |   |                              |
|   | Product code                        | 9509830   | ENT<br>entered   |                                     |   |                              |
|   | Finish                              | unknown   | ?<br>unknown     |                                     |   |                              |
|   | Size / configuration                | unknown   | ?<br>unknown     |                                     |   |                              |
|   | Handedness                          | unknown   | ?<br>unknown     |                                     |   |                              |
|   | components                          | unknown   | ?<br>unknown     |                                     |   |                              |
|   |                                     |   |                  |                                     |   |                              |
| Fixed glass screen (screen)   | footprint w × d (mm)                | 900 × 10   | ENT<br>entered   |                                     |   |                              |
|   | set-out                             | ?   | ?<br>unknown     |                                     |   | not set out from a wall face |
|   | project selection                   | unknown   | ?<br>unknown     |                                     |   |                              |
| Waste service points   |                                     |   |                  |                                     |   |                              |
| Toilet: Pan waste, S-trap (floor)   | service                             | waste   | ENT<br>entered   |                                     |   |                              |
|   | out from finished face (mm)         | 140–260   | PUB<br>published | finished face                       | American Standard M33158 Rev.03 install sheet: S-trap set-out 140–260 mm from the finished wall to the waste centre (260 nominal), on the pan centreline. A P-trap is 190 mm high instead  |                              |
|   | across from fixture centreline (mm) | 0   | PUB<br>published | fixture-centreline                  | American Standard M33158 Rev.03 install sheet: S-trap set-out 140–260 mm from the finished wall to the waste centre (260 nominal), on the pan centreline. A P-trap is 190 mm high instead  |                              |
|   | up from finished floor (mm)         | ?   | ?<br>unknown     |                                     |   | up height                    |
|   | along from end A (mm)               | 2650   | P<br>proposed    | wall_e end A                        |   |                              |
| Water service points   |                                     |   |                  |                                     |   |                              |
| Bath mixer and spout: Mixer body behind the hub (hot and cold inlets: spacing, size and depth are not on the set drawing)                   | service                             | water   | ENT<br>entered   |                                     |   |                              |
|   | out from finished face (mm)         | 0   | P<br>proposed    | finished face                       | Hub centre 60 mm right of the plate centre facing the wall (set drawing, derived) at the owner's proposed 750 mm plate centre                                                              |                              |
|   | across from fixture centreline (mm) | 60   | P<br>proposed    | fixture-centreline                  | Hub centre 60 mm right of the plate centre facing the wall (set drawing, derived) at the owner's proposed 750 mm plate centre                                                              |                              |
|   | up from finished floor (mm)         | 750   | P<br>proposed    | finished floor                      | Hub centre 60 mm right of the plate centre facing the wall (set drawing, derived) at the owner's proposed 750 mm plate centre                                                              |                              |
|   | along from end A (mm)               | 610   | P<br>proposed    | wall_e end A                        |   |                              |
| Shower system: G1/2 inlet at the upper wall rose (on the rail centreline)                                                                   | service                             | water   | ENT<br>entered   |                                     |   |                              |
|   | out from finished face (mm)         | 0   | P<br>proposed    | finished face                       | Y1173 drawing: G1/2 at the upper rose, 500 mm above the lower bracket; lower bracket at the owner's proposed 1200 mm (open), so 1700 mm                                                    |                              |
|   | across from fixture centreline (mm) | 0   | P<br>proposed    | fixture-centreline                  | Y1173 drawing: G1/2 at the upper rose, 500 mm above the lower bracket; lower bracket at the owner's proposed 1200 mm (open), so 1700 mm                                                    |                              |
|   | up from finished floor (mm)         | 1700   | P<br>proposed    | finished floor                      | Y1173 drawing: G1/2 at the upper rose, 500 mm above the lower bracket; lower bracket at the owner's proposed 1200 mm (open), so 1700 mm                                                    |                              |
|   | along from end A (mm)               | 2470   | P<br>proposed    | wall_w end A                        |   |                              |
| Shower mixer: Mixer body behind the plate (inlet layout and rough-in depth are not on the drawing; about 33.5 mm behind the plate, derived) | service                             | water   | ENT<br>entered   |                                     |   |                              |
|   | out from finished face (mm)         | 0   | P<br>proposed    | finished face                       | Plate centre at the owner's proposed 1000 mm; along the wall it is the drawn stand-in   |                              |
|   | across from fixture centreline (mm) | 0   | P<br>proposed    | fixture-centreline                  | Plate centre at the owner's proposed 1000 mm; along the wall it is the drawn stand-in   |                              |
|   | up from finished floor (mm)         | 1000   | P<br>proposed    | finished floor                      | Plate centre at the owner's proposed 1000 mm; along the wall it is the drawn stand-in   |                              |
|   | along from end A (mm)               | 2220   | E<br>estimated   | wall_w end A                        |   |                              |

| Element                             | Property                            | Value | Status        | Measured from      | Source   | Missing |
|-------------------------------------|-------------------------------------|-------|---------------|--------------------|---|---------|
| Toilet: Cold water point (stop tap) | service                             | water | ENT entered   |                    |   |         |
|                                     | out from finished face (mm)         | 0     | PUB published | finished face      | American Standard M33158 Rev.03 install sheet: cold water point 180 mm high, 180 mm left of the pan centreline facing it                                                                             |         |
|                                     | across from fixture centreline (mm) | -180  | PUB published | fixture-centreline | American Standard M33158 Rev.03 install sheet: cold water point 180 mm high, 180 mm left of the pan centreline facing it                                                                             |         |
|                                     | up from finished floor (mm)         | 180   | PUB published | finished floor     | American Standard M33158 Rev.03 install sheet: cold water point 180 mm high, 180 mm left of the pan centreline facing it                                                                             |         |
|                                     | along from end A (mm)               | 2470  | P proposed    | wall_e end A       |   |         |
| Power service points                |                                     |       |               |                    |   |         |
| Toilet: SpaLet seat power point     | service                             | power | ENT entered   |                    |   |         |
|                                     | out from finished face (mm)         | 0     | PUB published | finished face      | American Standard M33158 Rev.03 install sheet: SpaLet power point 300 mm high, 330 mm left of centre. Whether the seat gets its own outlet or reaches the moved vanity GPO is the electrician's call |         |
|                                     | across from fixture centreline (mm) | -330  | PUB published | fixture-centreline | American Standard M33158 Rev.03 install sheet: SpaLet power point 300 mm high, 330 mm left of centre. Whether the seat gets its own outlet or reaches the moved vanity GPO is the electrician's call |         |
|                                     | up from finished floor (mm)         | 300   | PUB published | finished floor     | American Standard M33158 Rev.03 install sheet: SpaLet power point 300 mm high, 330 mm left of centre. Whether the seat gets its own outlet or reaches the moved vanity GPO is the electrician's call |         |
|                                     | along from end A (mm)               | 2320  | P proposed    | wall_e end A       |   |         |

Unresolved in this view (76)

- Bathroom: Lauxes Next Gen 35 channel 1000 × 100 × 35, brushed nickel, 50 mm outlet WO50-BN: finished level at waste (mm) unknown; printed as "?" (missing finished level at waste (mm)).
- Bathroom: Lauxes Next Gen 35 channel 1000 × 100 × 35, brushed nickel, 50 mm outlet WO50-BN: outlet position unknown; printed as "?" (missing outlet position along the channel (entered on the waste), outlet sideways offset (brief)).
- Bathroom: Kano 316 tile-insert waste 120 × 120, brushed nickel, 50 mm outlet: finished level at waste (mm) unknown; printed as "?" (missing finished level at waste (mm)).
- Bathroom: Kano 316 tile-insert waste 120 × 120, brushed nickel, 50 mm outlet: body depth below grate (mm) unknown; printed as "?" (missing installation depth not in the Kano 316 Tile Insert Waste 120×120, brushed nickel brief).
- Bathroom: Kano 316 tile-insert waste 120 × 120, brushed nickel, 50 mm outlet: outlet position unknown; printed as "?" (missing outlet sideways offset, outlet from body back edge, body depth (envelope) (brief)).
- Corner bath (bath): set-out unknown; printed as "?" (missing not set out from a wall face).
- Corner bath (bath): wasteFromEnd unknown; printed as "?" (missing Sheet gives 520 mm from the right-angle corner along the bisector, not from the end. Along each wall that is 520/√2 ≈ 367.7 mm; that conversion is derived in the host-frame check, not entered as published wasteFromEnd.).
- Corner bath (bath): wasteEnd unknown; printed as "?" (missing Not entered from the cited source.).
- Corner bath (bath): wasteFromSide unknown; printed as "?" (missing Sheet gives 520 mm from the right-angle corner along the bisector, not from the side. Along each wall that is 520/√2 ≈ 367.7 mm; that conversion is derived in the host-frame check, not entered as published wasteFromSide.).
- Corner bath (bath): wasteConnectionDiameter unknown; printed as "?" (missing The Enflair drawing names a Ø50 waste hole, not a pipe connection or outlet size. No connection diameter is entered.).
- Corner bath (bath): surround unknown; printed as "?" (missing Not entered from the cited source.).
- Corner bath (bath): surroundDetail unknown; printed as "?" (missing Not entered from the cited source.).
- Bath mixer and spout (bath\_mixer): tapHoles unknown; printed as "?" (missing Not entered from the cited source.).
- Bath mixer and spout (bath\_mixer): holeLayout unknown; printed as "?" (missing Not entered from the cited source.).
- Bath mixer and spout (bath\_mixer): fixingLayout unknown; printed as "?" (missing Not entered from the cited source.).
- Bath mixer and spout (bath\_mixer): pressureMin unknown; printed as "?" (missing Not entered from the cited source.).
- Bath mixer and spout (bath\_mixer): inletMode unknown; printed as "?" (missing Not entered from the cited source.).
- Bath mixer and spout (bath\_mixer): inletSpacing unknown; printed as "?" (missing Not entered from the cited source.).
- Bath mixer and spout (bath\_mixer): inletOffset unknown; printed as "?" (missing Not entered from the cited source.).
- Bath mixer and spout (bath\_mixer): inletDepth unknown; printed as "?" (missing Not entered from the cited source.).
- Bath mixer and spout (bath\_mixer): inletHeight unknown; printed as "?" (missing Not entered from the cited source.).
- Bath mixer and spout (bath\_mixer): concealedDepthMin unknown; printed as "?" (missing Not entered from the cited source.).
- Bath mixer and spout (bath\_mixer): concealedDepthMax unknown; printed as "?" (missing Not entered from the cited source.).
- Bath waste (bath\_waste): set-out unknown; printed as "?" (missing not set out from a wall face).
- Bath waste (bath\_waste): width unknown; printed as "?" (missing Not entered from the cited source.).
- Bath waste (bath\_waste): depth unknown; printed as "?" (missing Not entered from the cited source.).
- Bath waste (bath\_waste): height unknown; printed as "?" (missing Not entered from the cited source.).
- Bath waste (bath\_waste): outletDiameter unknown; printed as "?" (missing Carton prints 40 mm nominal connection; no manufacturer sheet, so not entered as a published figure).
- Bath waste (bath\_waste): overflow unknown; printed as "?" (missing Not entered from the cited source.).
- Basin mixer (basin\_mixer): set-out unknown; printed as "?" (missing not set out from a wall face).
- Basin mixer (basin\_mixer): fixingLayout unknown; printed as "?" (missing Not entered from the cited source.).
- Basin mixer (basin\_mixer): pressureMin unknown; printed as "?" (missing Not entered from the cited source.).
- Basin mixer (basin\_mixer): inletMode unknown; printed as "?" (missing Not entered from the cited source.).
- Basin mixer (basin\_mixer): inletSpacing unknown; printed as "?" (missing Not entered from the cited source.).
- Basin mixer (basin\_mixer): waterConnection unknown; printed as "?" (missing Not entered from the cited source.).
- Basin mixer (basin\_mixer): inletOffset unknown; printed as "?" (missing Not entered from the cited source.).
- Basin mixer (basin\_mixer): inletDepth unknown; printed as "?" (missing Not entered from the cited source.).
- Basin mixer (basin\_mixer): inletHeight unknown; printed as "?" (missing Not entered from the cited source.).
- Basin mixer (basin\_mixer): concealedDepthMin unknown; printed as "?" (missing Not entered from the cited source.).
- Basin mixer (basin\_mixer): concealedDepthMax unknown; printed as "?" (missing Not entered from the cited source.).
- Shower system (shower\_system): pressureMin unknown; printed as "?" (missing Not entered from the cited source.).
- Shower system (shower\_system): pressureMax unknown; printed as "?" (missing Not entered from the cited source.).
- Shower system (shower\_system): temperatureMax unknown; printed as "?" (missing Not entered from the cited source.).
- Shower system (shower\_system): adjustmentMin unknown; printed as "?" (missing Not entered from the cited source.).
- Shower system (shower\_system): adjustmentMax unknown; printed as "?" (missing Not entered from the cited source.).
- Shower system (shower\_system): inletOffset unknown; printed as "?" (missing Not entered from the cited source.).
- Shower system (shower\_system): inletDepth unknown; printed as "?" (missing Not entered from the cited source.).
- Shower system (shower\_system): inletHeight unknown; printed as "?" (missing Not entered from the cited source.).
- Shower mixer (shower\_mixer): width unknown; printed as "?" (missing Owner's copy of the Enflair K1130 drawing gives plate Ø65; it has no web link, so it is not entered as a published brief figure (the figures are on the measures).).
- Shower mixer (shower\_mixer): depth unknown; printed as "?" (missing Owner's copy of the Enflair K1130 drawing gives 65.5 mm lever to plate plus the 4 mm plate; no web link, so not entered as a published brief figure.).
- Shower mixer (shower\_mixer): height unknown; printed as "?" (missing Derived from the owner's copy of the Enflair K1130 drawing (Ø65 plate, Ø45 hub, 107 mm lever); no web link, so not entered as a published brief figure.).
- Shower mixer (shower\_mixer): mounting unknown; printed as "?" (missing Not entered from the cited source.).
- Shower mixer (shower\_mixer): tapHoles unknown; printed as "?" (missing Not entered from the cited source.).
- Shower mixer (shower\_mixer): holeLayout unknown; printed as "?" (missing Not entered from the cited source.).
- Shower mixer (shower\_mixer): fixingLayout unknown; printed as "?" (missing Not entered from the cited source.).
- Shower mixer (shower\_mixer): pressureMin unknown; printed as "?" (missing Not entered from the cited source.).
- Shower mixer (shower\_mixer): inletMode unknown; printed as "?" (missing Not entered from the cited source.).
- Shower mixer (shower\_mixer): inletSpacing unknown; printed as "?" (missing Not entered from the cited source.).
- Shower mixer (shower\_mixer): waterConnection unknown; printed as "?" (missing Not entered from the cited source.).
- Shower mixer (shower\_mixer): inletOffset unknown; printed as "?" (missing Not entered from the cited source.).
- Shower mixer (shower\_mixer): inletDepth unknown; printed as "?" (missing Not entered from the cited source.).
- Shower mixer (shower\_mixer): inletHeight unknown; printed as "?" (missing Not entered from the cited source.).
- Shower mixer (shower\_mixer): concealedDepthMin unknown; printed as "?" (missing Not entered from the cited source.).
- Shower mixer (shower\_mixer): concealedDepthMax unknown; printed as "?" (missing Not entered from the cited source.).

- Towel rail (towel\_rail): fixingCentresWidth unknown; printed as "?" (missing Not entered from the cited source.).
- Towel rail (towel\_rail): powerOffset unknown; printed as "?" (missing Not entered from the cited source.).
- Towel rail (towel\_rail): powerHeight unknown; printed as "?" (missing Not entered from the cited source.).
- Towel rail (towel\_rail): powerDepth unknown; printed as "?" (missing Not entered from the cited source.).
- Towel rail (towel\_rail): waterConnection unknown; printed as "?" (missing Not entered from the cited source.).
- Towel rail (towel\_rail\_2): fixingCentresWidth unknown; printed as "?" (missing Not entered from the cited source.).
- Towel rail (towel\_rail\_2): powerOffset unknown; printed as "?" (missing Not entered from the cited source.).
- Towel rail (towel\_rail\_2): powerHeight unknown; printed as "?" (missing Not entered from the cited source.).
- Towel rail (towel\_rail\_2): powerDepth unknown; printed as "?" (missing Not entered from the cited source.).
- Towel rail (towel\_rail\_2): waterConnection unknown; printed as "?" (missing Not entered from the cited source.).
- Toilet: Pan waste, S-trap (floor): up from finished floor (mm) unknown; printed as "?" (missing up height).
- Fixed glass screen (screen): set-out unknown; printed as "?" (missing not set out from a wall face).